



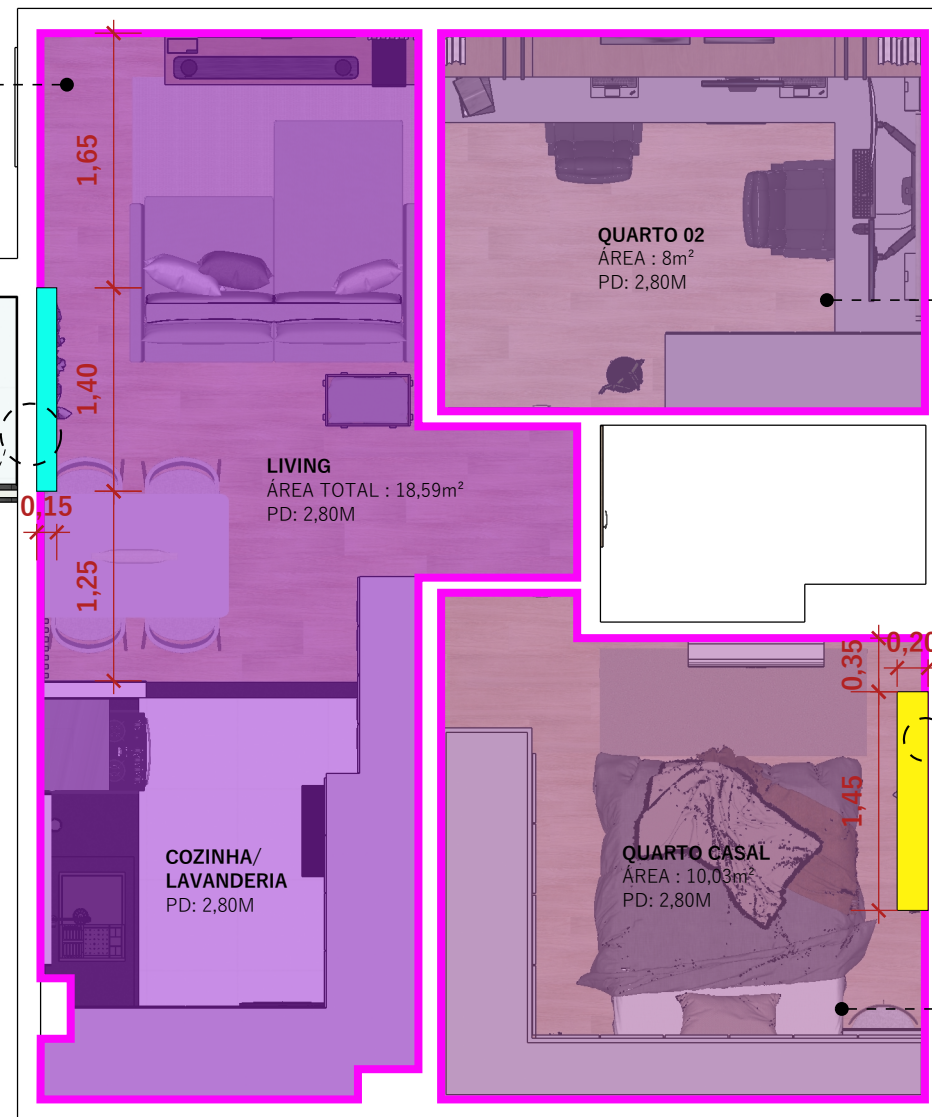

DET 01:
CORTINEIRO COM
ILUMINAÇÃO INDIRETA
CORTINA COM TRILHO SUÍÇO


LEGENDA DE GESSO	
	REBAIXO DE FORRO DE GESSO TABICADO COM ALTURA ATÉ 10CM
	CORTINEIRO COM ILUMINAÇÃO INDIRETA (CONFERIR E CONSIDERAR 10CM A MAIS DA PORTA)
	CORTINEIRO COM ILUMINAÇÃO INDIRETA (CONFERIR E CONSIDERAR 10CM A MAIS DA JANELA)
PÉ DIREITO ENTREGUE 2,80m PÉ DIREITO COM GESSO REBAIXADO 2,70m	

ACABAMENTO EM TINTA ACRÍLICA
FOSCA BRANCO SUVINIL

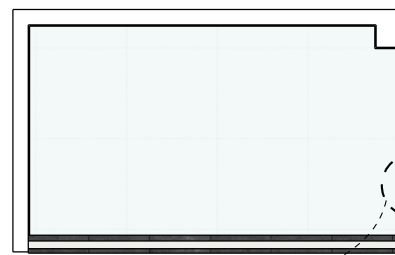

PLANTA DE GESSO
ESC 1:50

PREVER ESTRUTURAÇÃO DO FORRO DE GESSO PARA
QUE NÃO ATRAPALHE A INSTALAÇÃO DAS LUMINÁRIAS
E PERFIS DE LED - VERIFICAR PONTOS E MEDIDAS NA
PLANTA DE LUMINOTÉCNICO

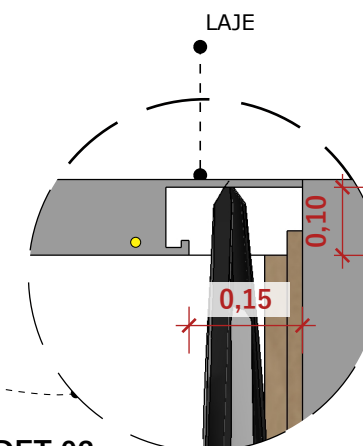

DET 02:
ESCALA 1:10
CORTINA COM TRILHO SUÍÇO

ACABAMENTO EM TINTA ACRÍLICA
FOSCA BRANCO SUVINIL



@STEFANIEFELIX.INTERIORES

****CONFERIR TODAS AS MEDIDAS NO LOCAL****
A DESIGNER NÃO SE RESPONSABILIZA POR
DIFERENÇAS DE MEDIDAS ENTRE PROJETO E OBRA;
VALOR DA COTA PREVALECE SOBRE A ESCALA;
DÚVIDAS FALAR COM A DESIGNER.

SF.STEFANIEFELIX@GMAIL.COM


PROJETO DE INTERIORES
PLANTA DE GESSO

CLIENTE
GUSTAVO PATATIVA
DESIGNER
STEFANIE FELIX

(19) 99577-3340

LOCAL
MRV - LUZ DO CAMPO
DATA
26/04/2024

FOLHA
03/15

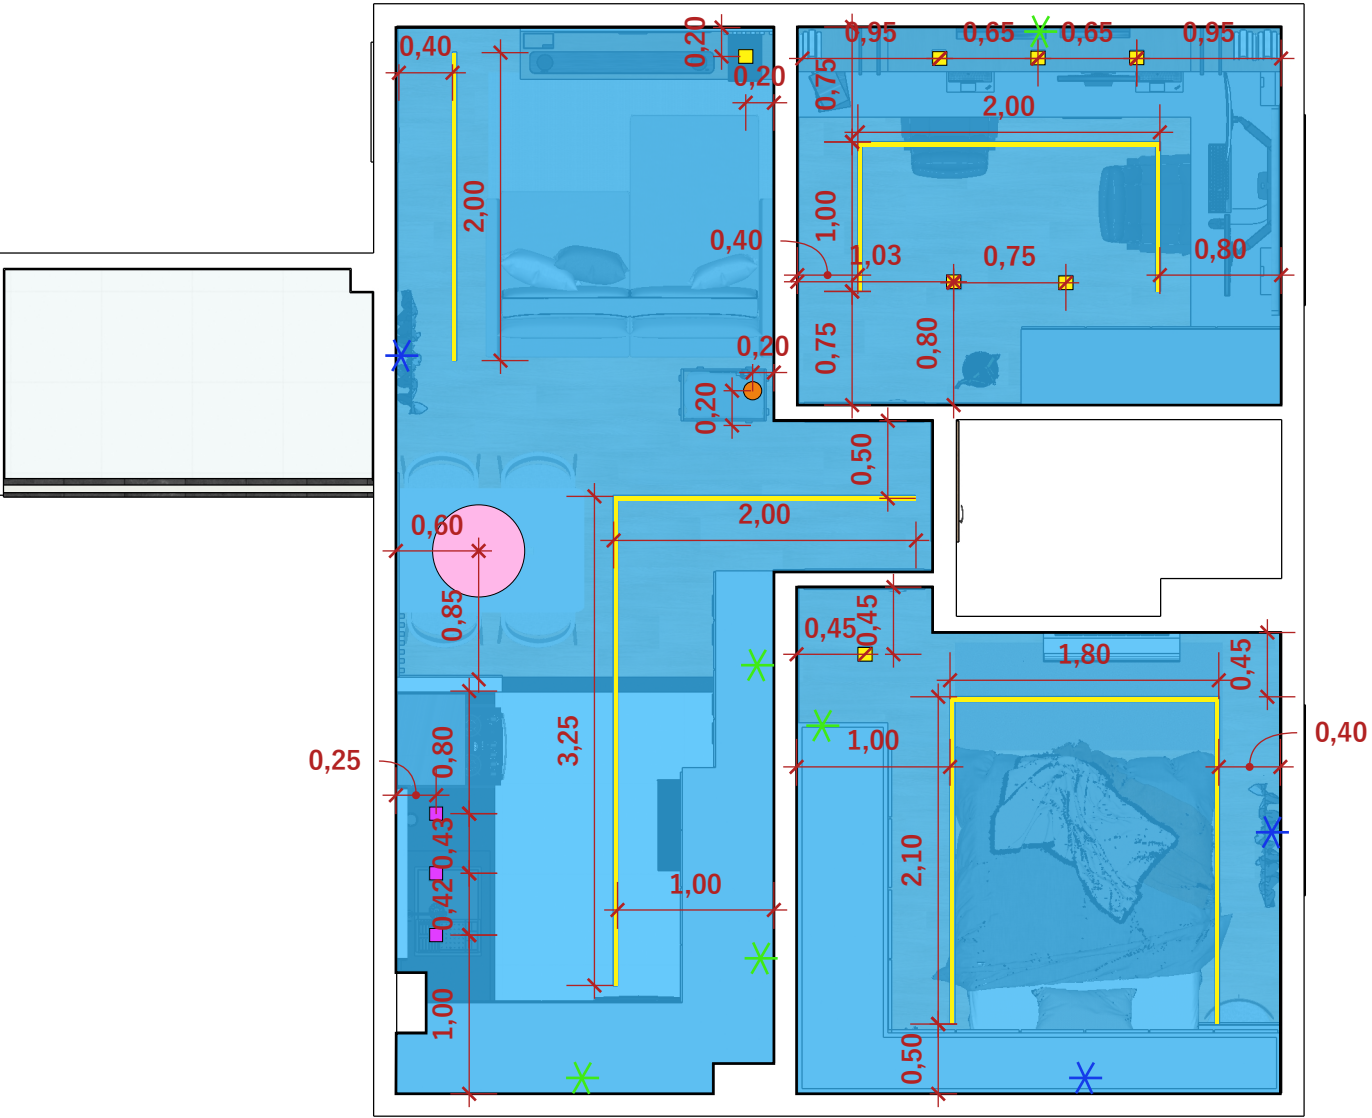

PLANTA LUMINOTÉCNICA
ESC 1:50

LEGENDA	
	PERFIL DE ALUMINIO EMBUTIR DE POLICARBONATO COM FITA FULL LED 24V PRO 1450 LUMENS/M 4000K - 17,5 METROS (SUGESTÃO MARCA STELLA)
	FITA DE LED 12V ECO 10W 700 LUMENS/M 3000K 3 MTS (SUGESTÃO MARCA STELLA)
	PERFIL DE ALUMINIO EMBUTIR NA MARCENARIA DE POLICARBONATO COM FITA DE LED 12V ECO 700 LUMENS/M - 3000K - 6,5 METROS (CONFERIR DETALHAMENTO)
	LUSTRE PENDENTE HORIZON SNAIL PRETO - 1UN
	SPOT MR11 EVO MINI DICROICA DIRECIONAVEIS 4000K 3W 36° - 10UN / SUGESTÃO MARCA STELLA
	SPOT MR16 ECO 4000K 4W 350 LUMENS 36°60° - 3UN / SUGESTÃO MARCA STELLA
	SPOT CANNON MINI MR11 DIRECIONÁVEL PRETO FOSCO COR 3000L - 1UN



@STEFANIEFELIX.INTERIORES

****CONFERIR TODAS AS MEDIDAS NO LOCAL****
A DESIGNER NÃO SE RESPONSABILIZA POR DIFERENÇAS DE MEDIDAS ENTRE PROJETO E OBRA; VALOR DA COTA PREVALECE SOBRE A ESCALA; DÚVIDAS FALAR COM A DESIGNER.

SF.STEFANIEFELIX@GMAIL.COM

PROJETO DE INTERIORES

PLANTA DE LUMINOTÉCNICO E CIRCUÍTO

CLIENTE
GUSTAVO PATATIVA

DESIGNER
STEFANIE FELIX

(19) 99577-3340

LOCAL
MRV - LUZ DO CAMPO

DATA
26/04/2024

FOLHA

04/15