



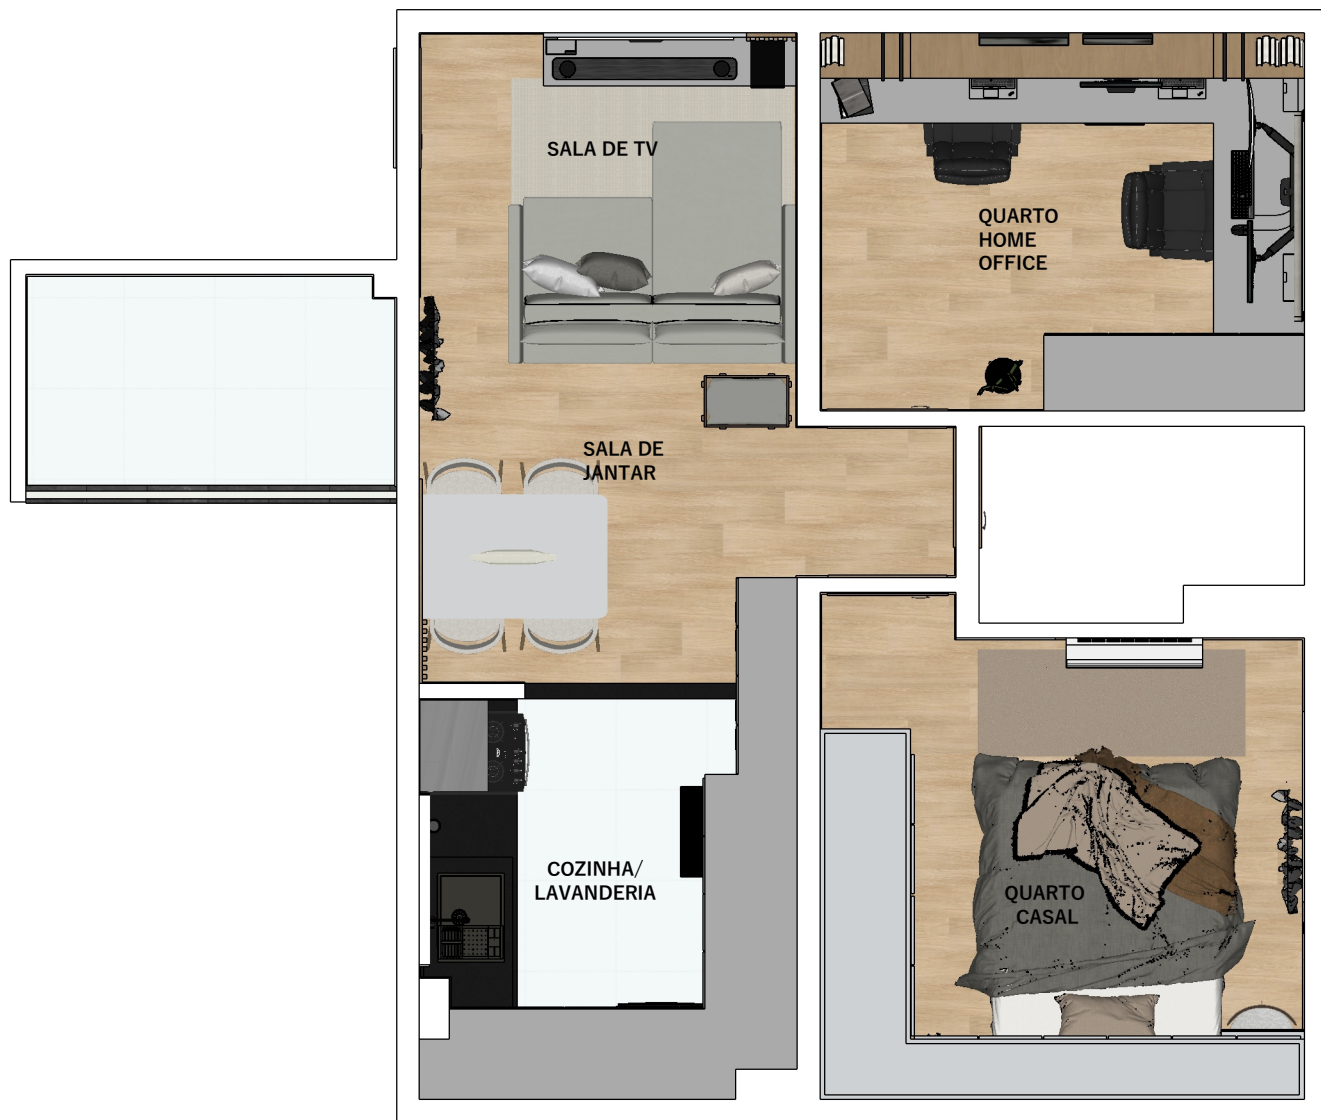

PLANTA BAIXA HUMANIZADA
ESC 1:50

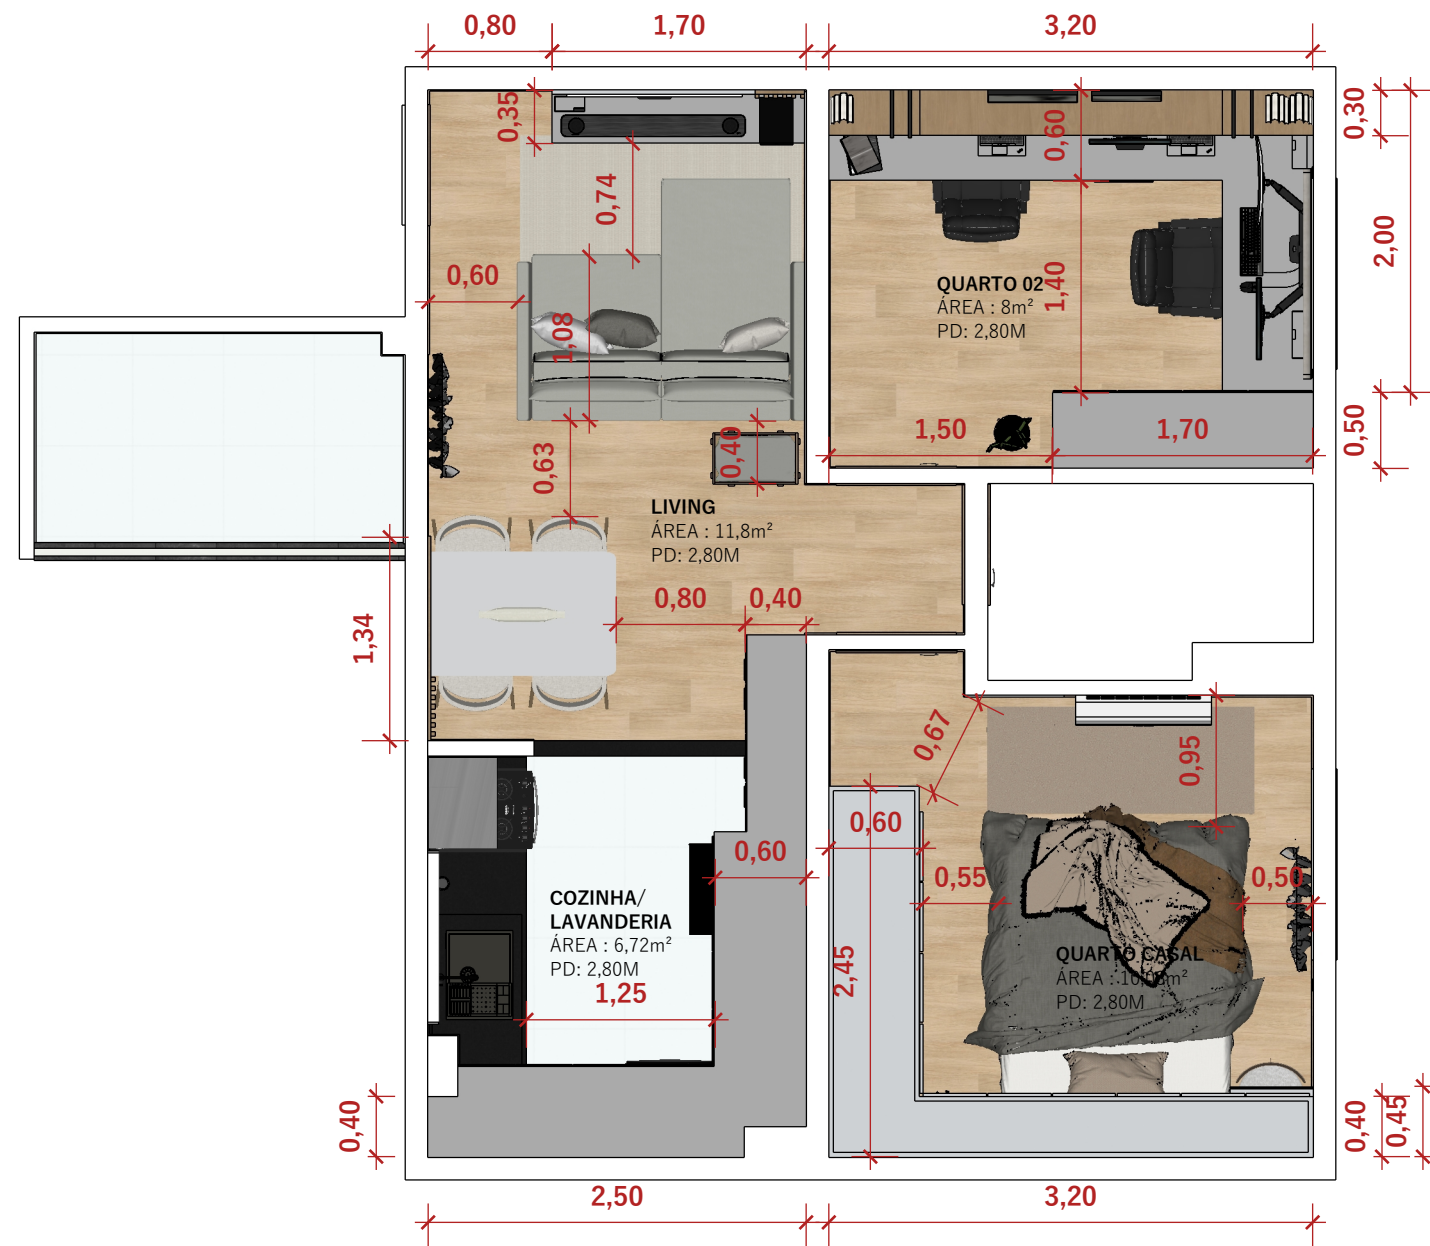

PLANTA BAIXA EXECUTIVA
ESC 1:50



@STEFANIEFELIX.INTERIORES

****CONFERIR TODAS AS MEDIDAS NO LOCAL****
A DESIGNER NÃO SE RESPONSABILIZA POR
DIFERENÇAS DE MEDIDAS ENTRE PROJETO E OBRA;
VALOR DA COTA PREVALECE SOBRE A ESCALA;
DÚVIDAS FALAR COM A DESIGNER.

SF.STEFANIEFELIX@GMAIL.COM

PROJETO DE INTERIORES

PLANTA BAIXA HUMANIZADA/EXECUTIVA

CLIENTE
GUSTAVO PATATIVA


DESIGNER
STEFANIE FELIX

(19) 99577-3340

LOCAL
MRV - LUZ DO CAMPO

DATA
26/04/2024


FOLHA
01/15

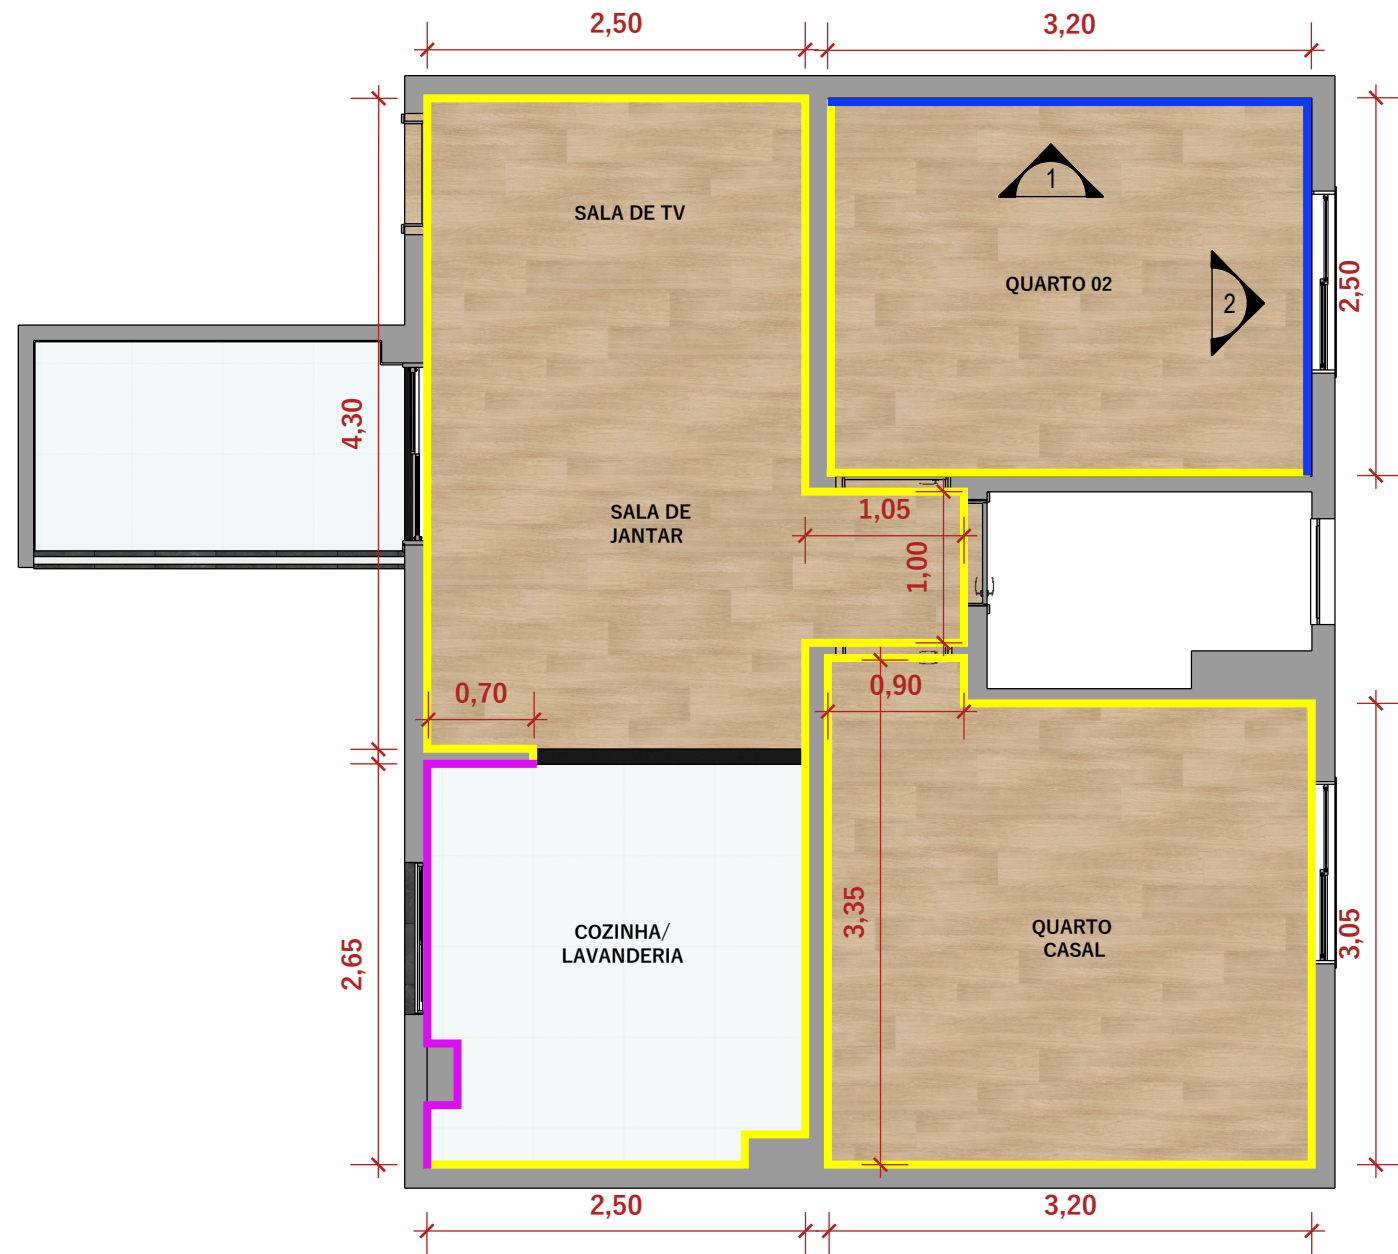


PLANTA BAIXA - ACABAMENTOS
ESC 1:50

LEGENDA DE ACABAMENTOS	
	ACABAMENTO EM PINTURA TINTA LAVAVEL COR GEADA - BRANCO GATINHO OU ESCONDERIJO SILENCIOSO - CORAL (LAVÁVEL) 95m²
	PINTURA COR CIMENTO QUEIMADO - AVENIDA EXPRESSA SUVINIL - 14,69m²
	REVESTIMENTO EXISTENTE BRANCO h=1,50m

PÉ DIREITO ENTREGUE 2,80m
PÉ DIREITO COM GESSO REBAIXADO 2,70m

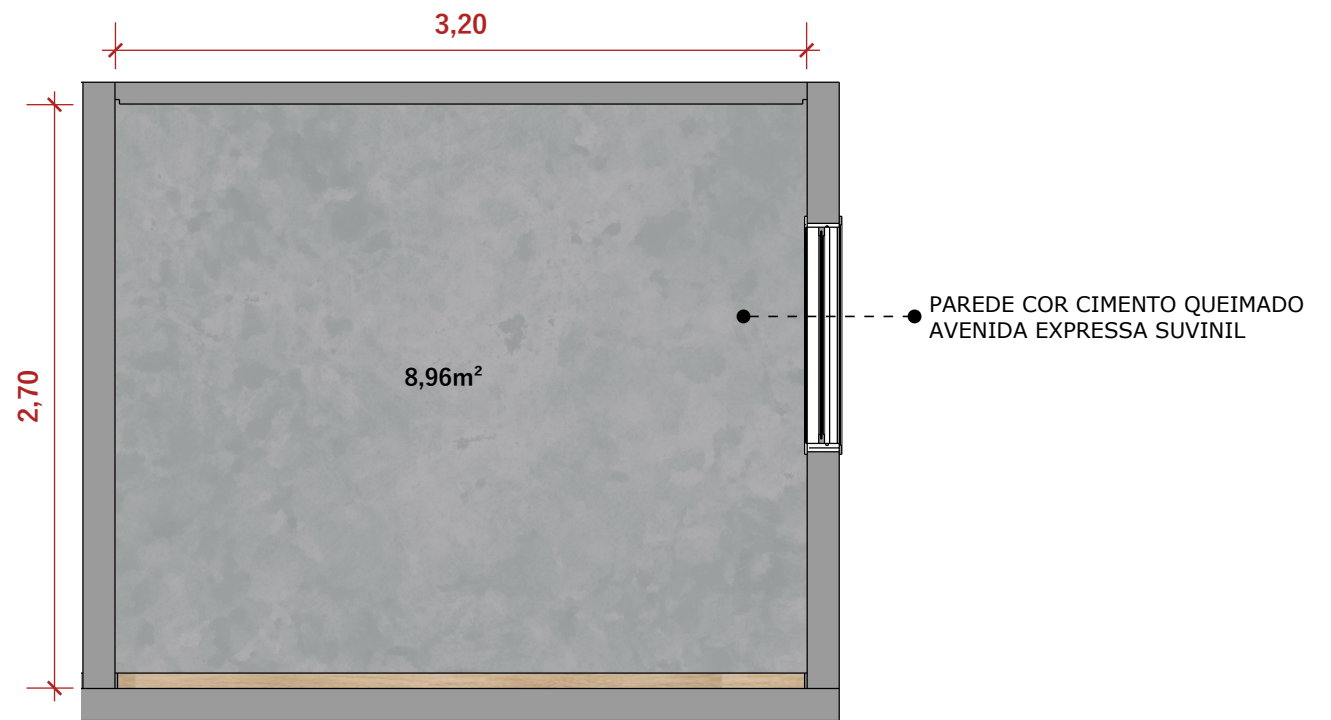

VISTA 1 - HOME OFFICE
ESC 1:35

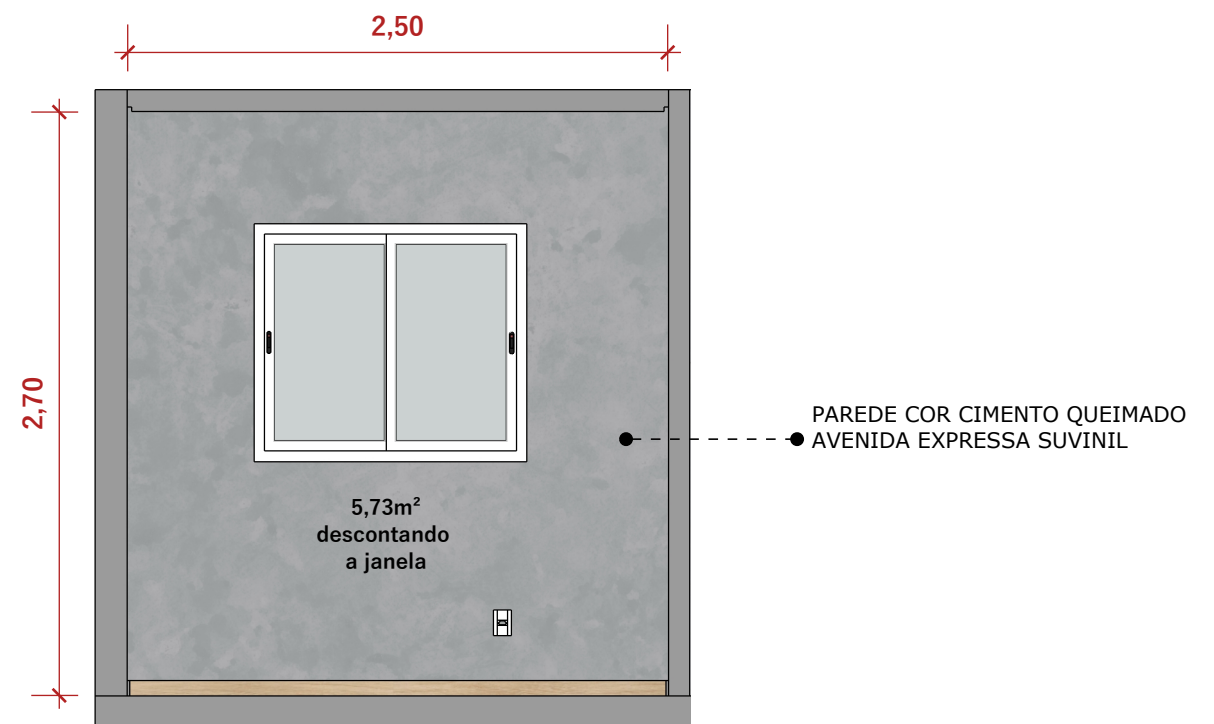

VISTA 2 - HOME OFFICE
ESC 1:35



@STEFANIEFELIX.INTERIORES

****CONFERIR TODAS AS MEDIDAS NO LOCAL****
A DESIGNER NÃO SE RESPONSABILIZA POR DIFERENÇAS DE MEDIDAS ENTRE PROJETO E OBRA; VALOR DA COTA PREVALECE SOBRE A ESCALA; DÚVIDAS FALAR COM A DESIGNER.

SF.STEFANIEFELIX@GMAIL.COM

PROJETO DE INTERIORES
PLANTA DE ACABAMENTOS

CLIENTE
GUSTAVO PATATIVA
DESIGNER
STEFANIE FELIX

(19) 99577-3340

LOCAL
MRV - LUZ DO CAMPO
DATA
26/04/2024



FOLHA
02/15



DET 01:
CORTINEIRO COM
ILUMINAÇÃO INDIRETA
CORTINA COM TRILHO SUÍÇO


LEGENDA DE GESSO	
	REBAIXO DE FORRO DE GESSO TABICADO COM ALTURA ATÉ 10CM
	CORTINEIRO COM ILUMINAÇÃO INDIRETA (CONFERIR E CONSIDERAR 10CM A MAIS DA PORTA)
	CORTINEIRO COM ILUMINAÇÃO INDIRETA (CONFERIR E CONSIDERAR 10CM A MAIS DA JANELA)
PÉ DIREITO ENTREGUE 2,80m PÉ DIREITO COM GESSO REBAIXADO 2,70m	

ACABAMENTO EM TINTA ACRÍLICA
FOSCA BRANCO SUVINIL

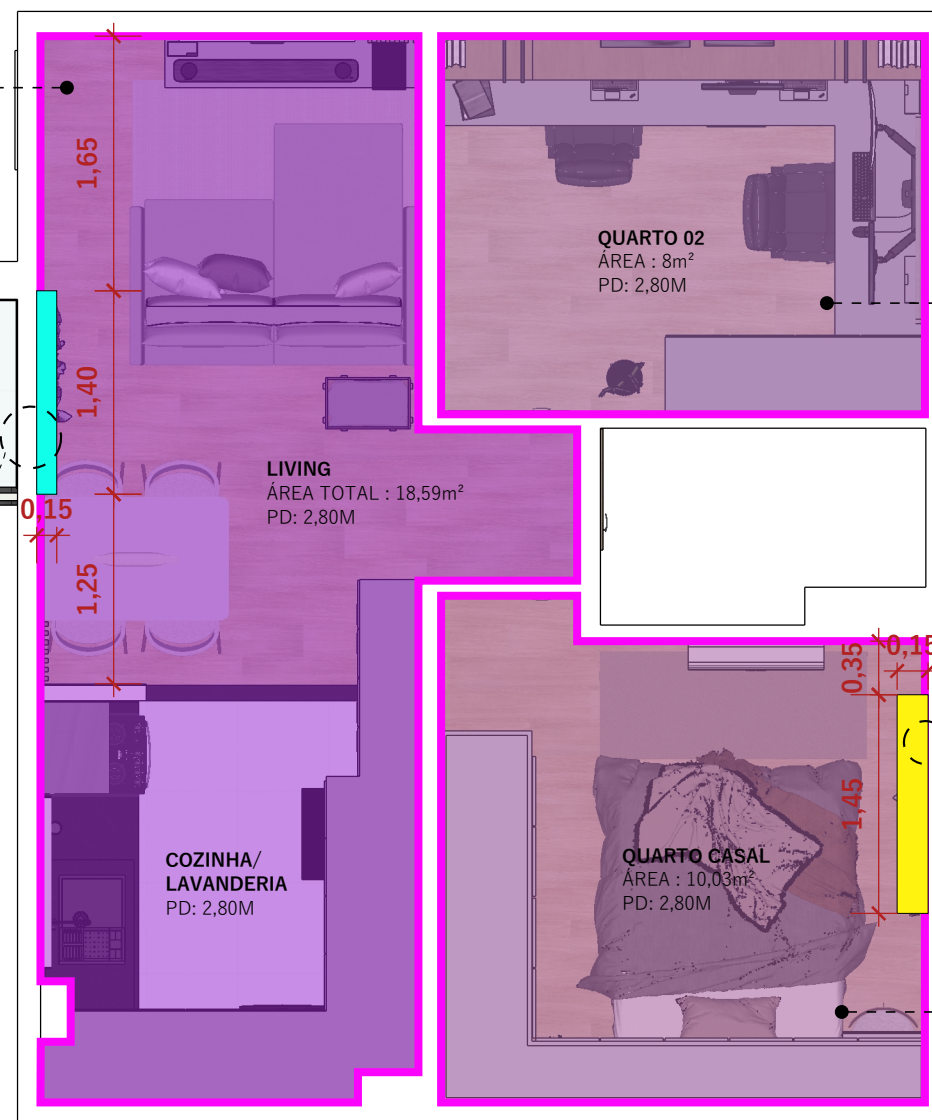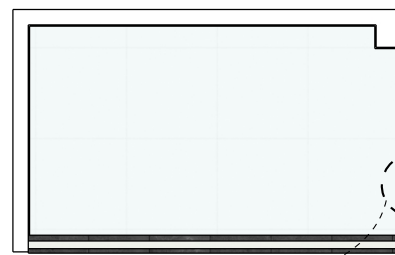

PLANTA DE GESSO
ESC 1:50

PREVER ESTRUTURAÇÃO DO FORRO DE GESSO PARA
QUE NÃO ATRAPALHE A INSTALAÇÃO DAS LUMINÁRIAS
E PERFIS DE LED - VERIFICAR PONTOS E MEDIDAS NA
PLANTA DE LUMINOTÉCNICO

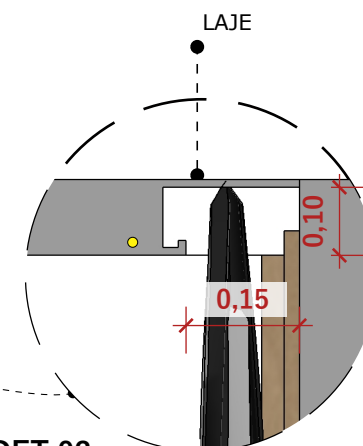

DET 02:
ESCALA 1:10
CORTINA COM TRILHO SUÍÇO

ACABAMENTO EM TINTA ACRÍLICA
FOSCA BRANCO SUVINIL



@STEFANIEFELIX.INTERIORES

****CONFERIR TODAS AS MEDIDAS NO LOCAL****
A DESIGNER NÃO SE RESPONSABILIZA POR
DIFERENÇAS DE MEDIDAS ENTRE PROJETO E OBRA;
VALOR DA COTA PREVALECE SOBRE A ESCALA;
DÚVIDAS FALAR COM A DESIGNER.

SF.STEFANIEFELIX@GMAIL.COM

PROJETO DE INTERIORES
PLANTA DE GESSO


CLIENTE
GUSTAVO PATATIVA
DESIGNER
STEFANIE FELIX

(19) 99577-3340

LOCAL
MRV - LUZ DO CAMPO
DATA
26/04/2024


FOLHA
03/15

LEGENDA	
	PERFIL DE ALUMINIO EMBUTIR DE POLICARBONATO COM FITA FULL LED 24V PRO 1450 LUMENS/M 4000K - 17,5 METROS (SUGESTÃO MARCA STELLA)
	FITA DE LED 12V ECO 10W 700 LUMENS/M 3000K 3 MTS (SUGESTÃO MARCA STELLA)
	PERFIL DE ALUMINIO EMBUTIR NA MARCENARIA DE POLICARBONATO COM FITA DE LED 12V ECO 700 LUMENS/M - 3000K - 6,5 METROS (CONFERIR DETALHAMENTO)
	LUSTRE PENDENTE HORIZON SNAIL PRETO - 1UN
	SPOT MR11 EVO MINI DICROICA DIRECIONAVEIS 4000K 3W 36° - 10UN / SUGESTÃO MARCA STELLA
	SPOT MR16 ECO 4000K 4W 350 LUMENS 36°60° - 3UN / SUGESTÃO MARCA STELLA
	SPOT CANNON MINI MR11 DIRECIONÁVEL PRETO FOSCO COR 3000K - 1UN
	SPOT PAR 20 EVO DUPLO - 5,5W CADA - 25° / SUGESTÃO MARCA STELLA

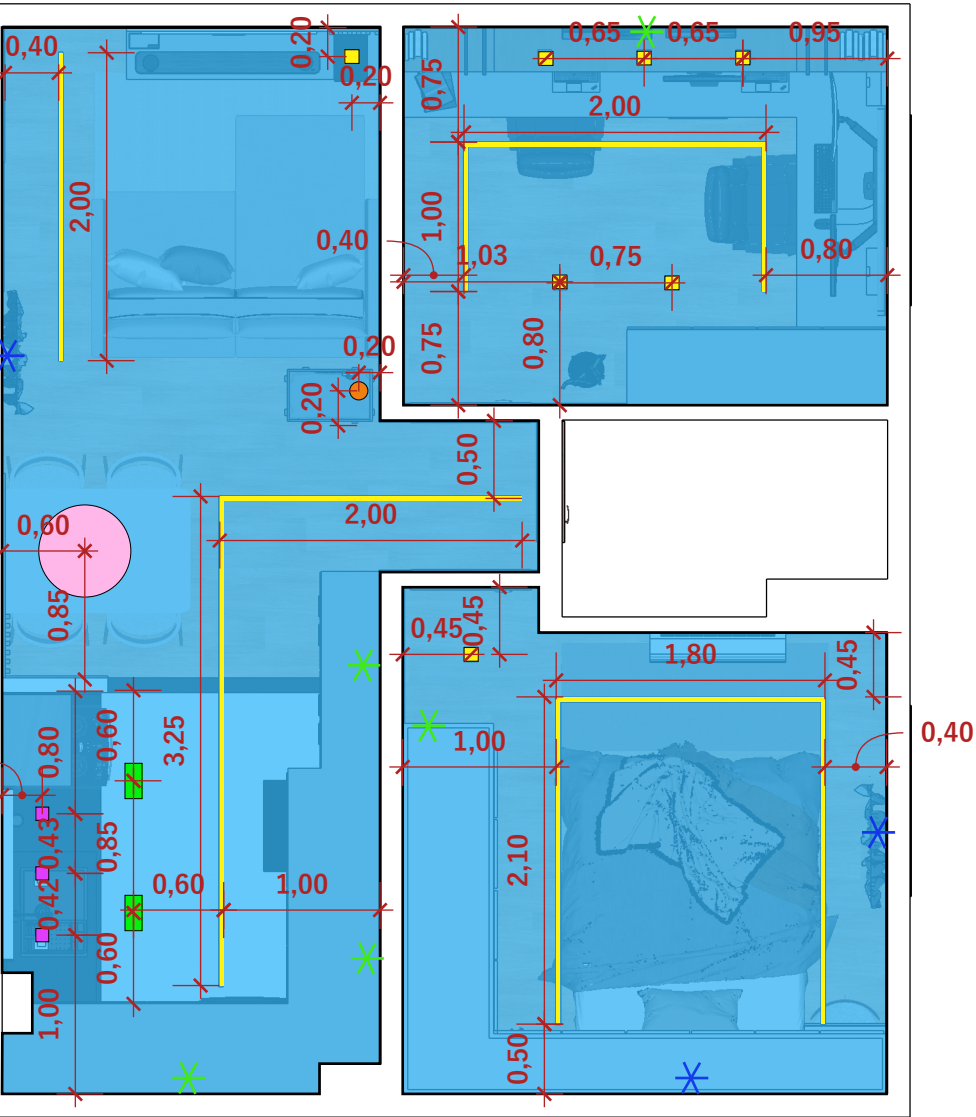

PLANTA LUMINOTÉCNICA
ESC 1:50

S - INTERRUPTOR
Nº - NÚMERO DO CIRCUITO

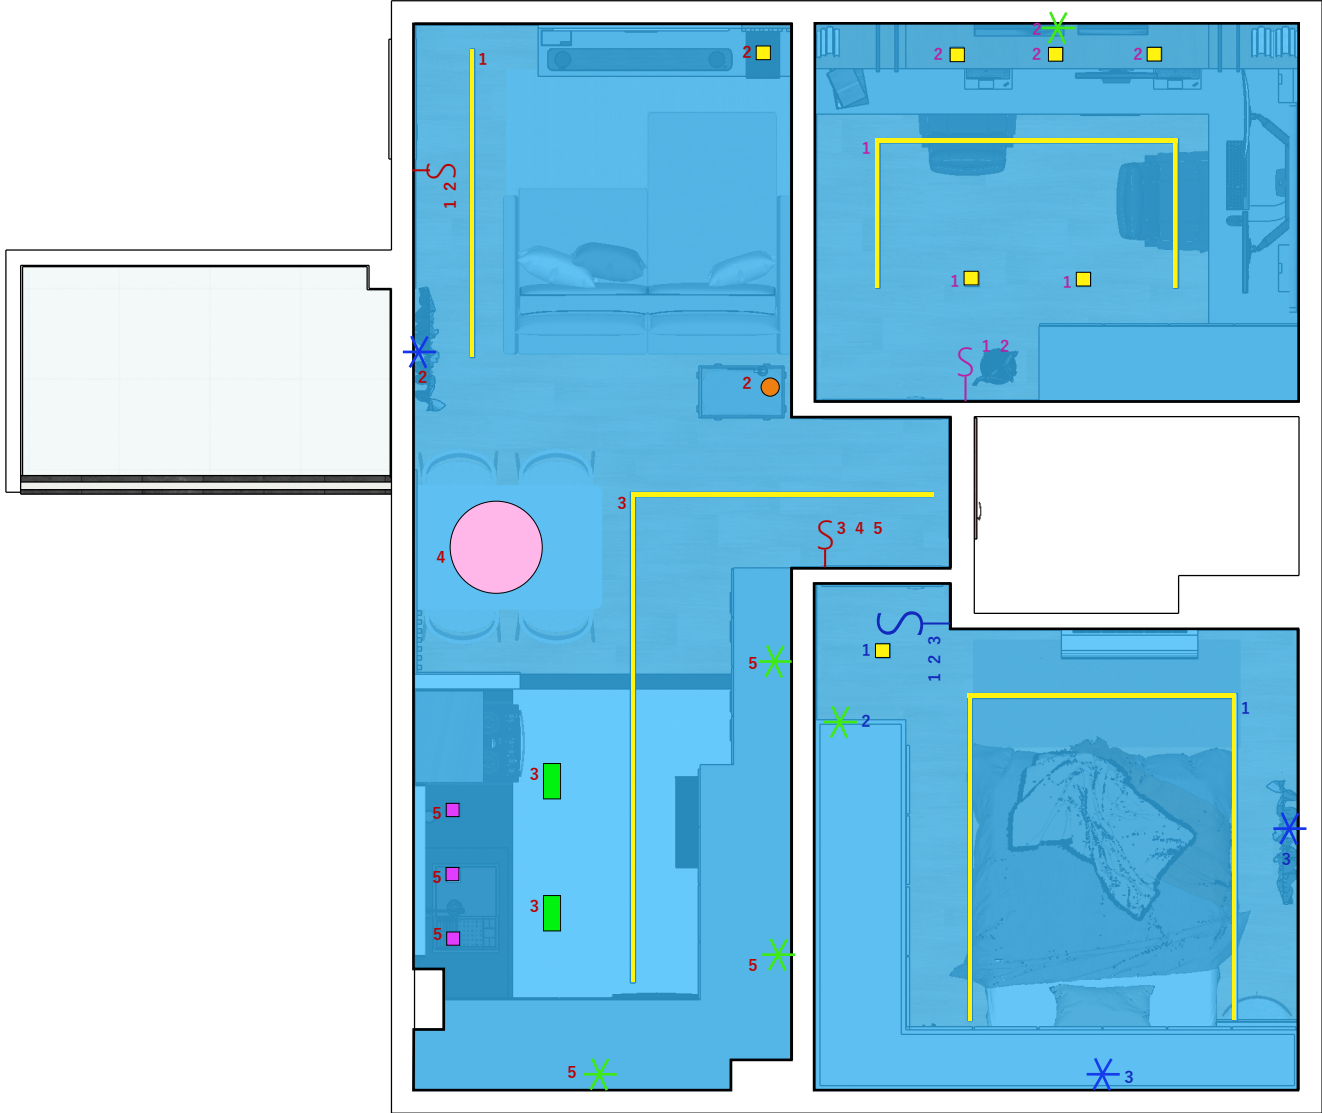

PLANTA CIRCUÍTO
ESC 1:50



@STEFANIEFELIX.INTERIORES

SF.STEFANIEFELIX@GMAIL.COM

****CONFERIR TODAS AS MEDIDAS NO LOCAL****
A DESIGNER NÃO SE RESPONSABILIZA POR DIFERENÇAS DE MEDIDAS ENTRE PROJETO E OBRA; VALOR DA COTA PREVALECE SOBRE A ESCALA; DÚVIDAS FALAR COM A DESIGNER.

PROJETO DE INTERIORES

PLANTA DE LUMINOTÉCNICO E CIRCUÍTO

CLIENTE
GUSTAVO PATATIVA

DESIGNER
STEFANIE FELIX


LOCAL
MRV - LUZ DO CAMPO

DATA
26/04/2024

FOLHA

04/15

(19) 99577-3340

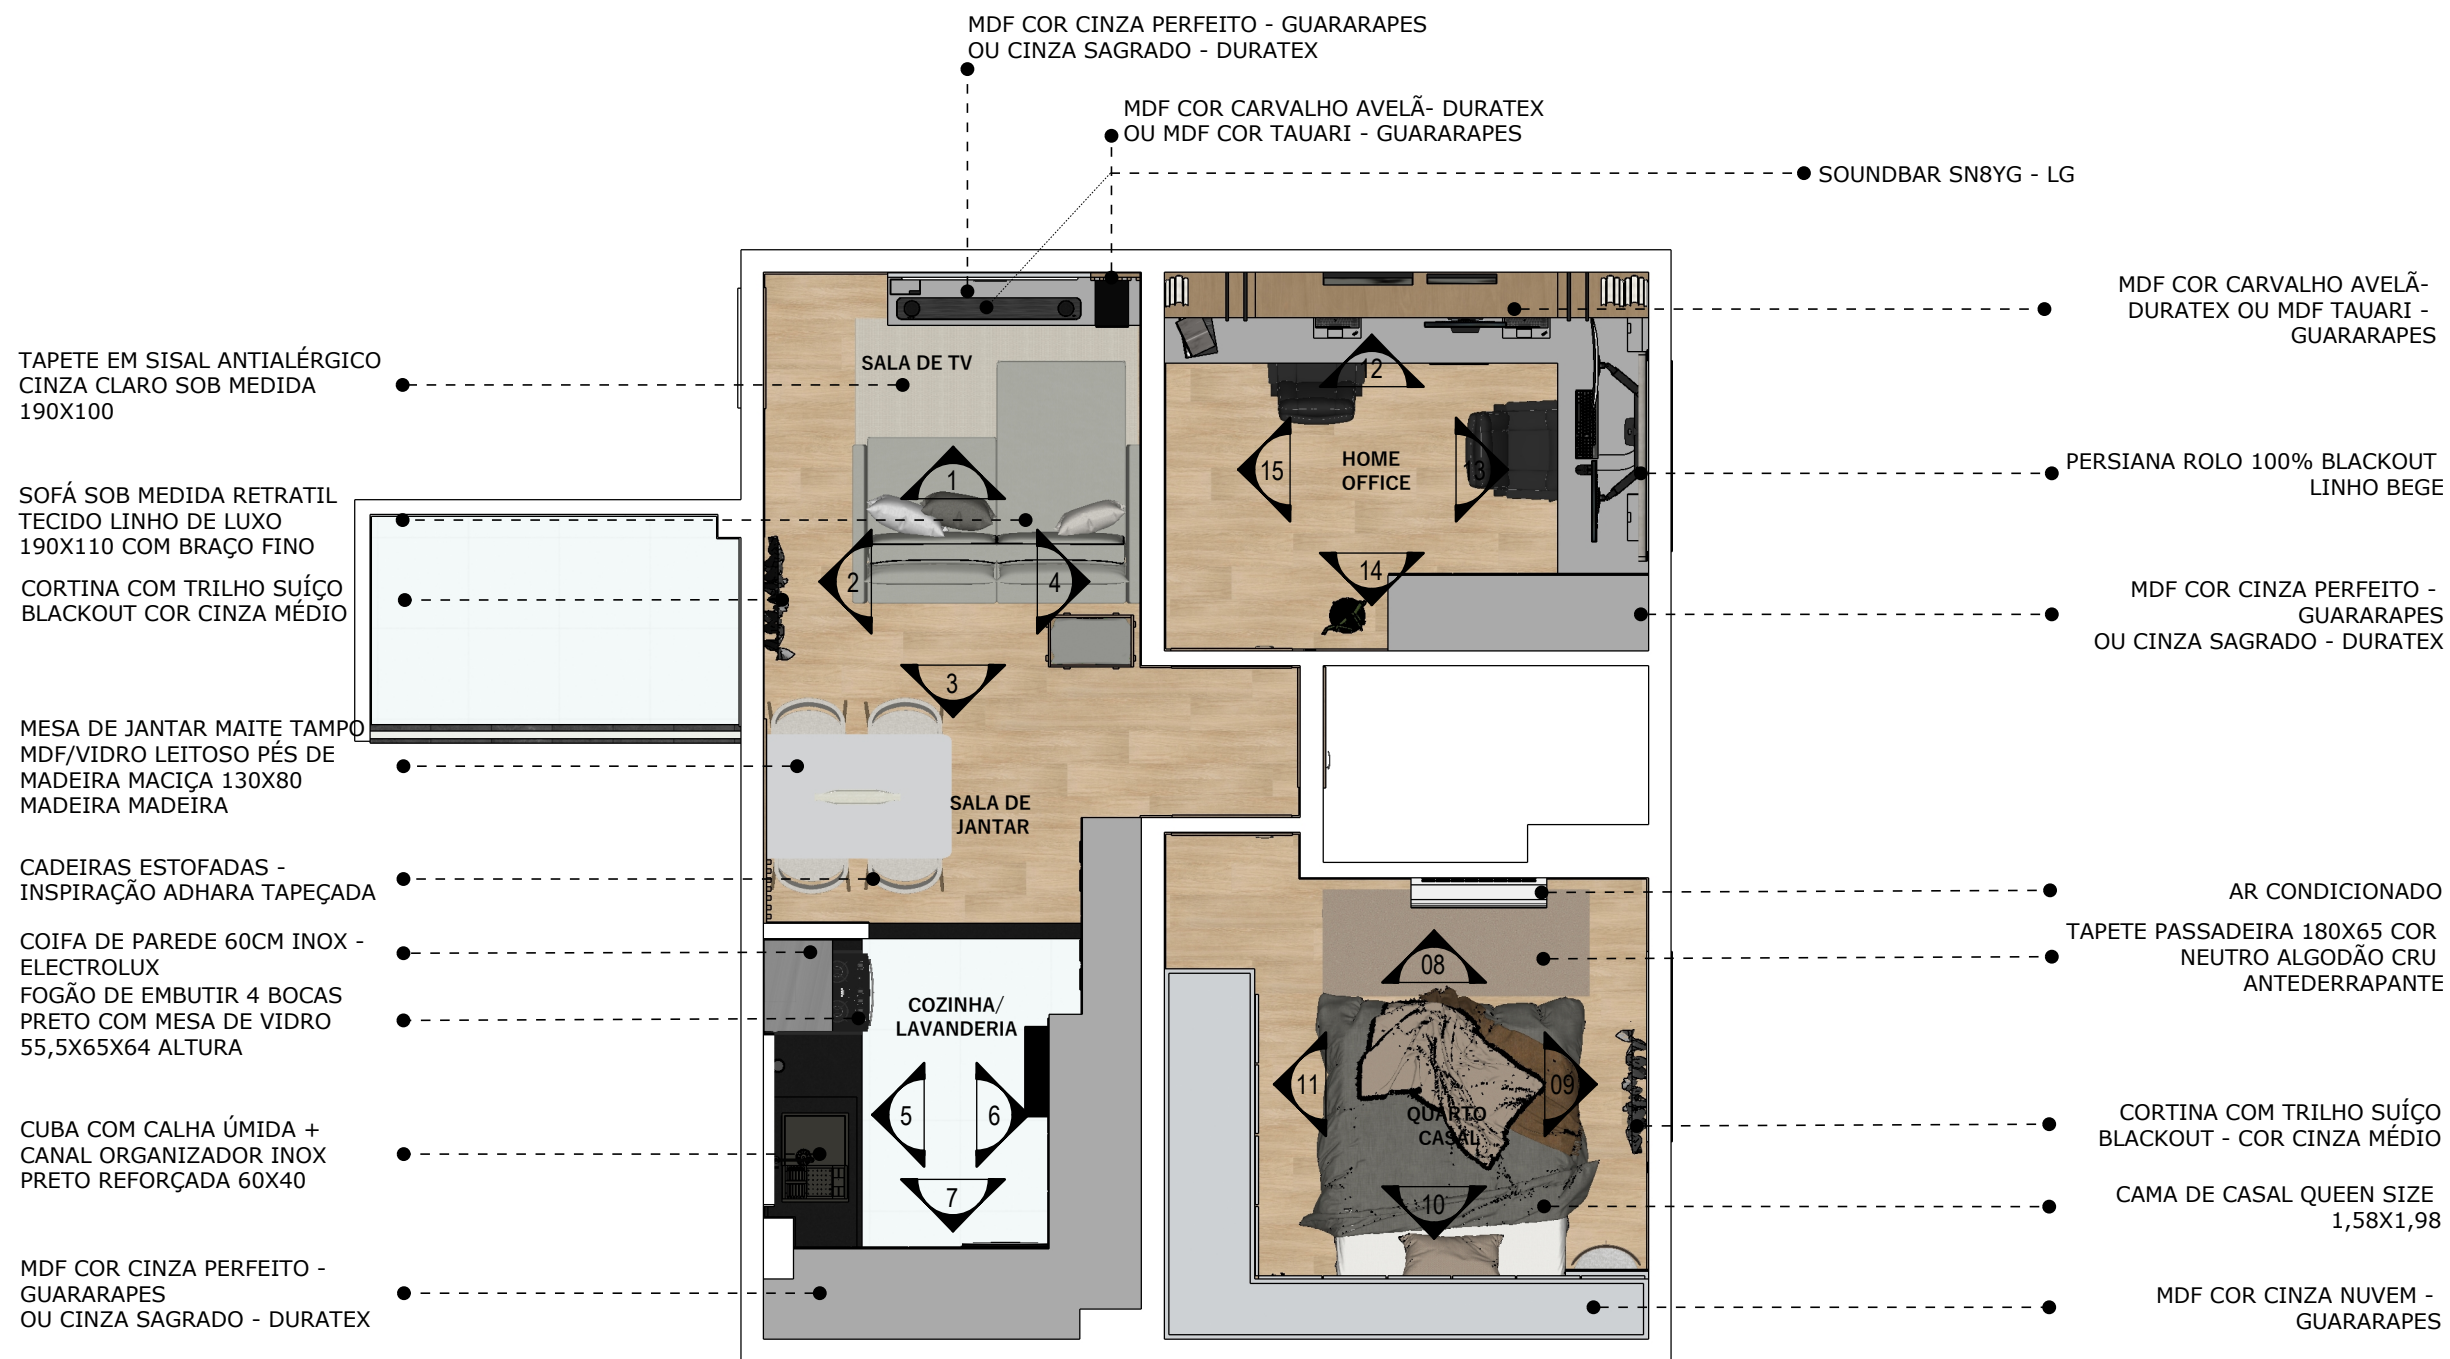

01 PLANTA DE LAYOUT
ESC 1:50



****CONFERIR TODAS AS MEDIDAS NO LOCAL****
A DESIGNER NÃO SE RESPONSABILIZA POR DIFERENÇAS DE MEDIDAS ENTRE PROJETO E OBRA; VALOR DA COTA PREVALECE SOBRE A ESCALA; DÚVIDAS FALAR COM A DESIGNER.


PROJETO DE INTERIORES
PLANTA BAIXA LAYOUT

CLIENTE
GUSTAVO PATATIVA
DESIGNER
STEFANIE FELIX

LOCAL
MRV - LUZ DO CAMPO
DATA
26/04/2024

FOLHA
05/15

LIVING - SALA DE TV E JANTAR

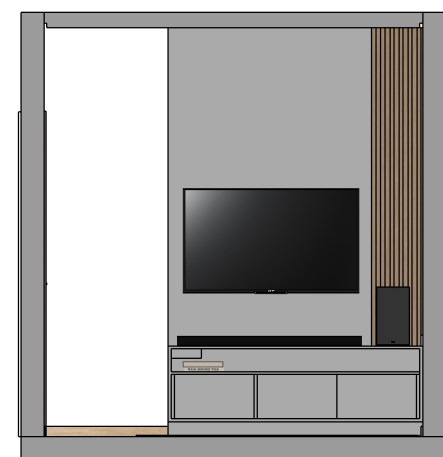


01 VISTA 01
ESC 1:50





02 VISTA 02
ESC 1:50



03 VISTA 03
ESC 1:50

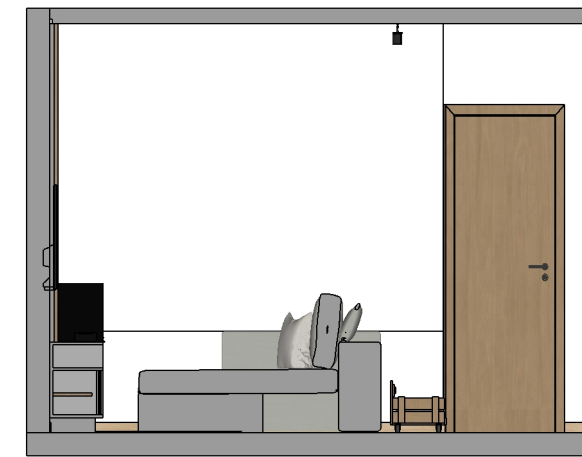

04 VISTA 04
ESC 1:50

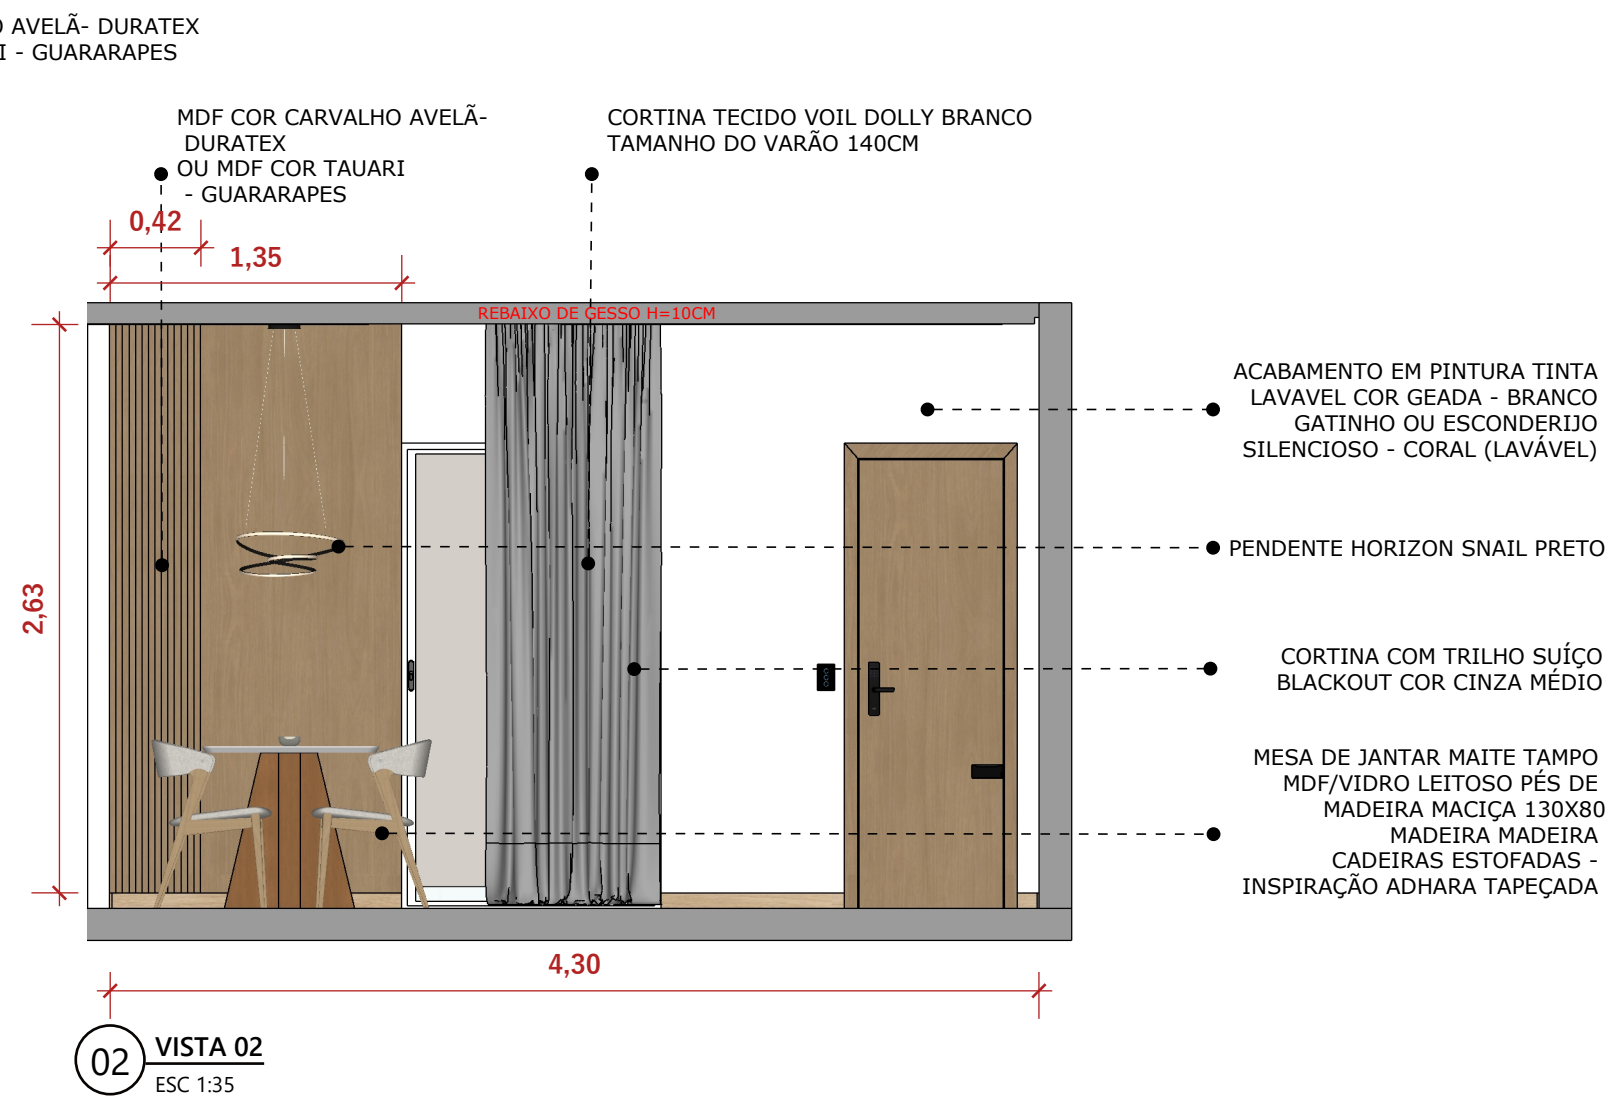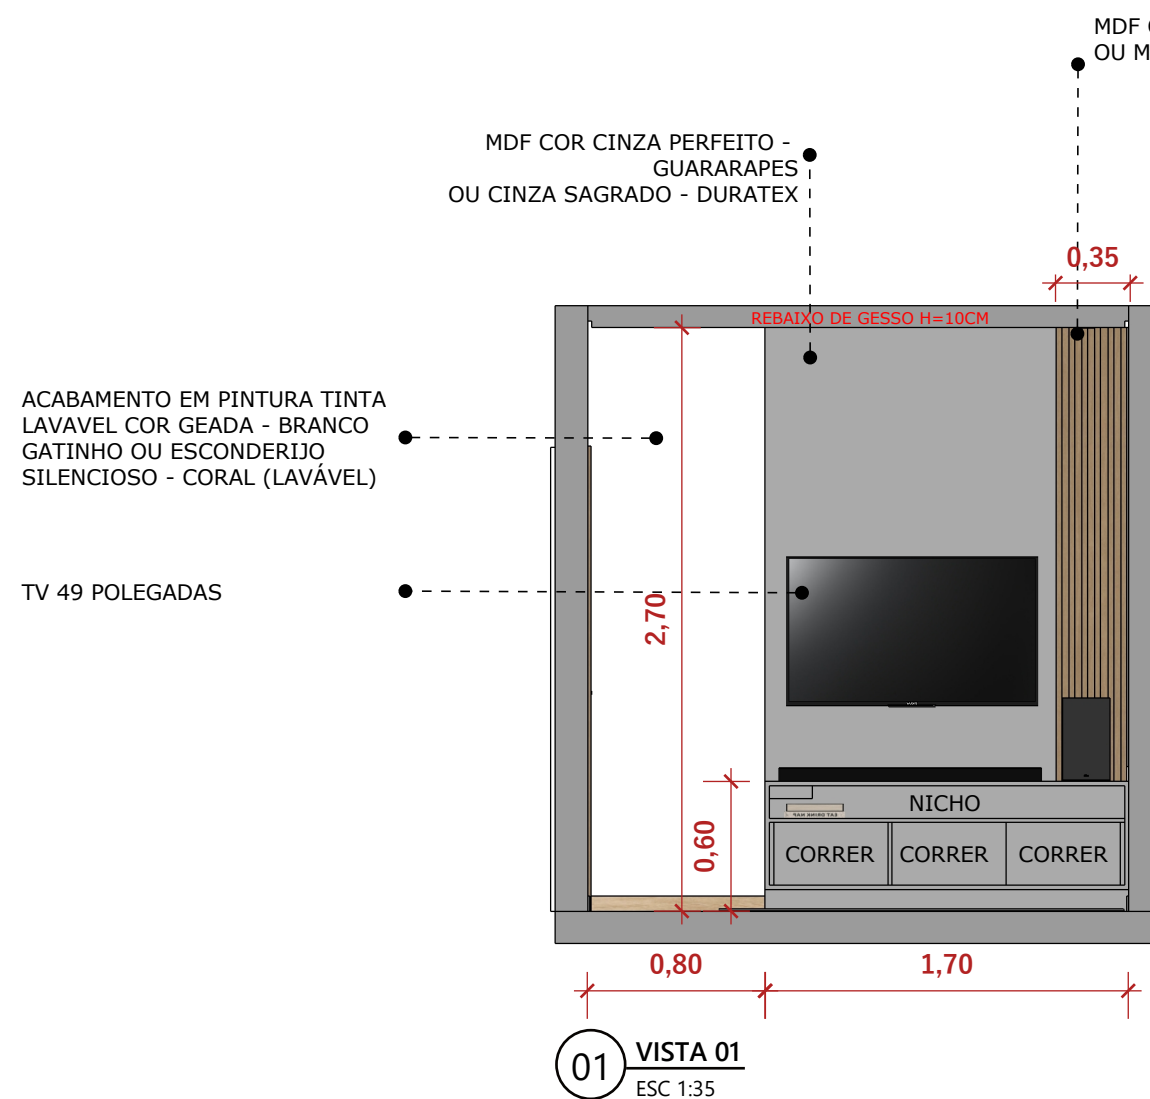

@STEFANIEFELIX.INTERIORES

****CONFERIR TODAS AS MEDIDAS NO LOCAL****
A DESIGNER NÃO SE RESPONSABILIZA POR
DIFERENÇAS DE MEDIDAS ENTRE PROJETO E OBRA;
VALOR DA COTA PREVALECE SOBRE A ESCALA;
DÚVIDAS FALAR COM A DESIGNER.

SF.STEFANIEFELIX@GMAIL.COM

PROJETO DE INTERIORES

LIVING - VISTAS HUMANIZADAS E COM COTAS

CLIENTE
GUSTAVO PATATIVA

DESIGNER
STEFANIE FELIX




(19) 99577-3340

LOCAL
MRV - LUZ DO CAMPO


DATA
26/04/2024

FOLHA
06/15


LIVING - SALA DE TV E JANTAR

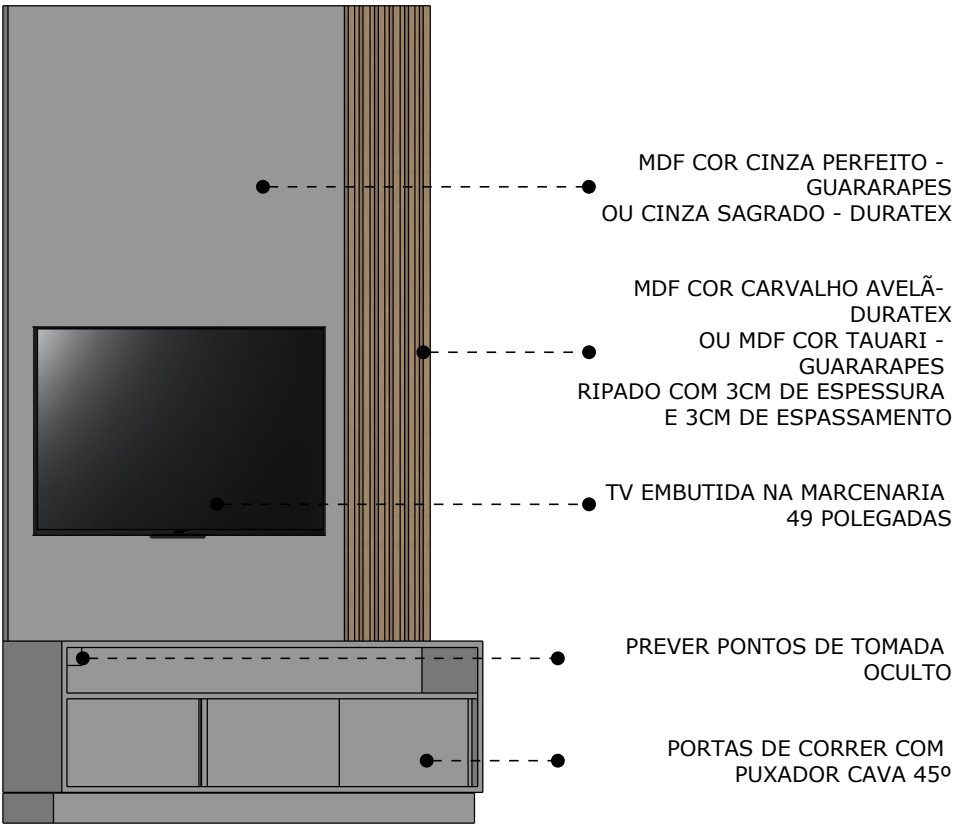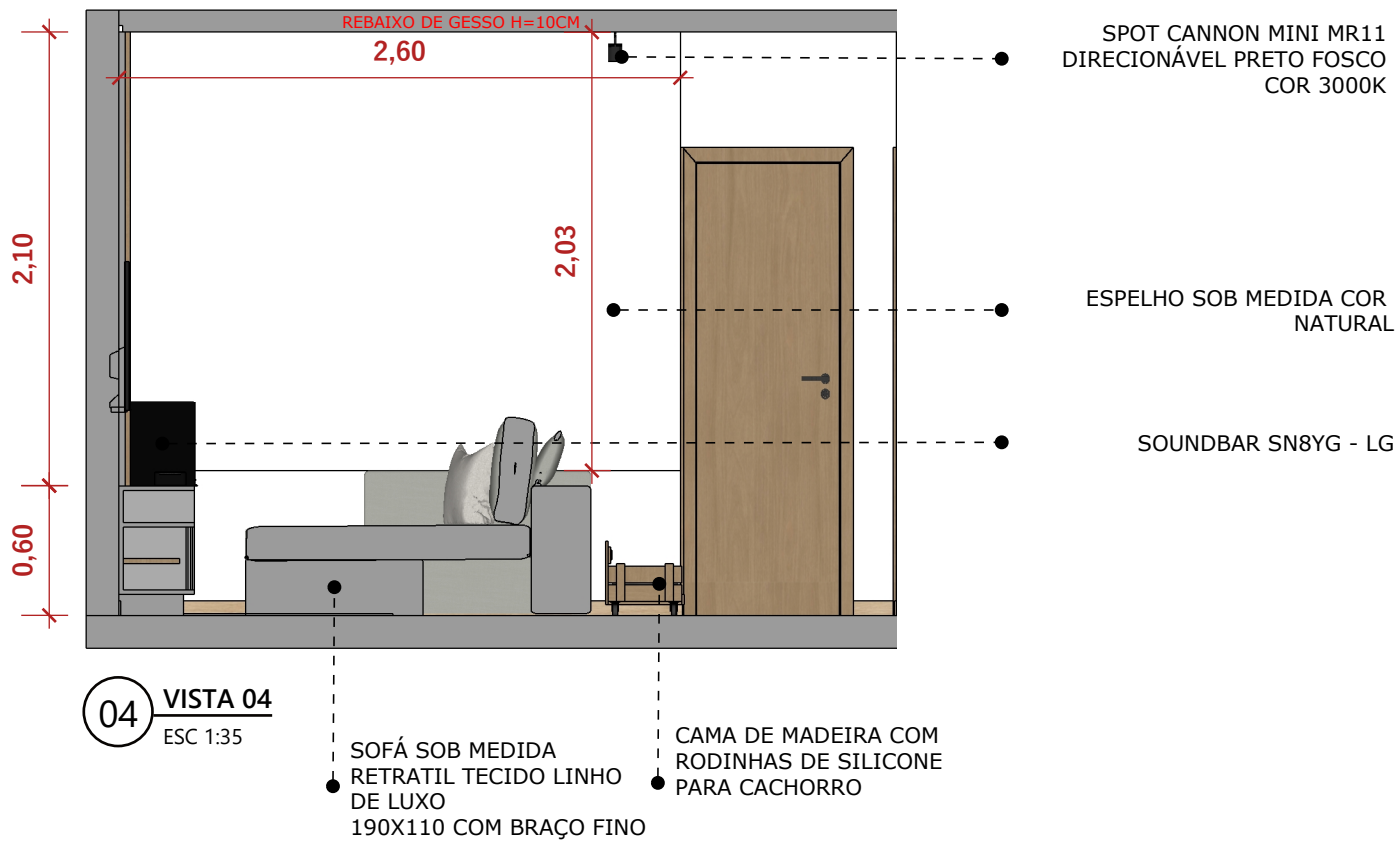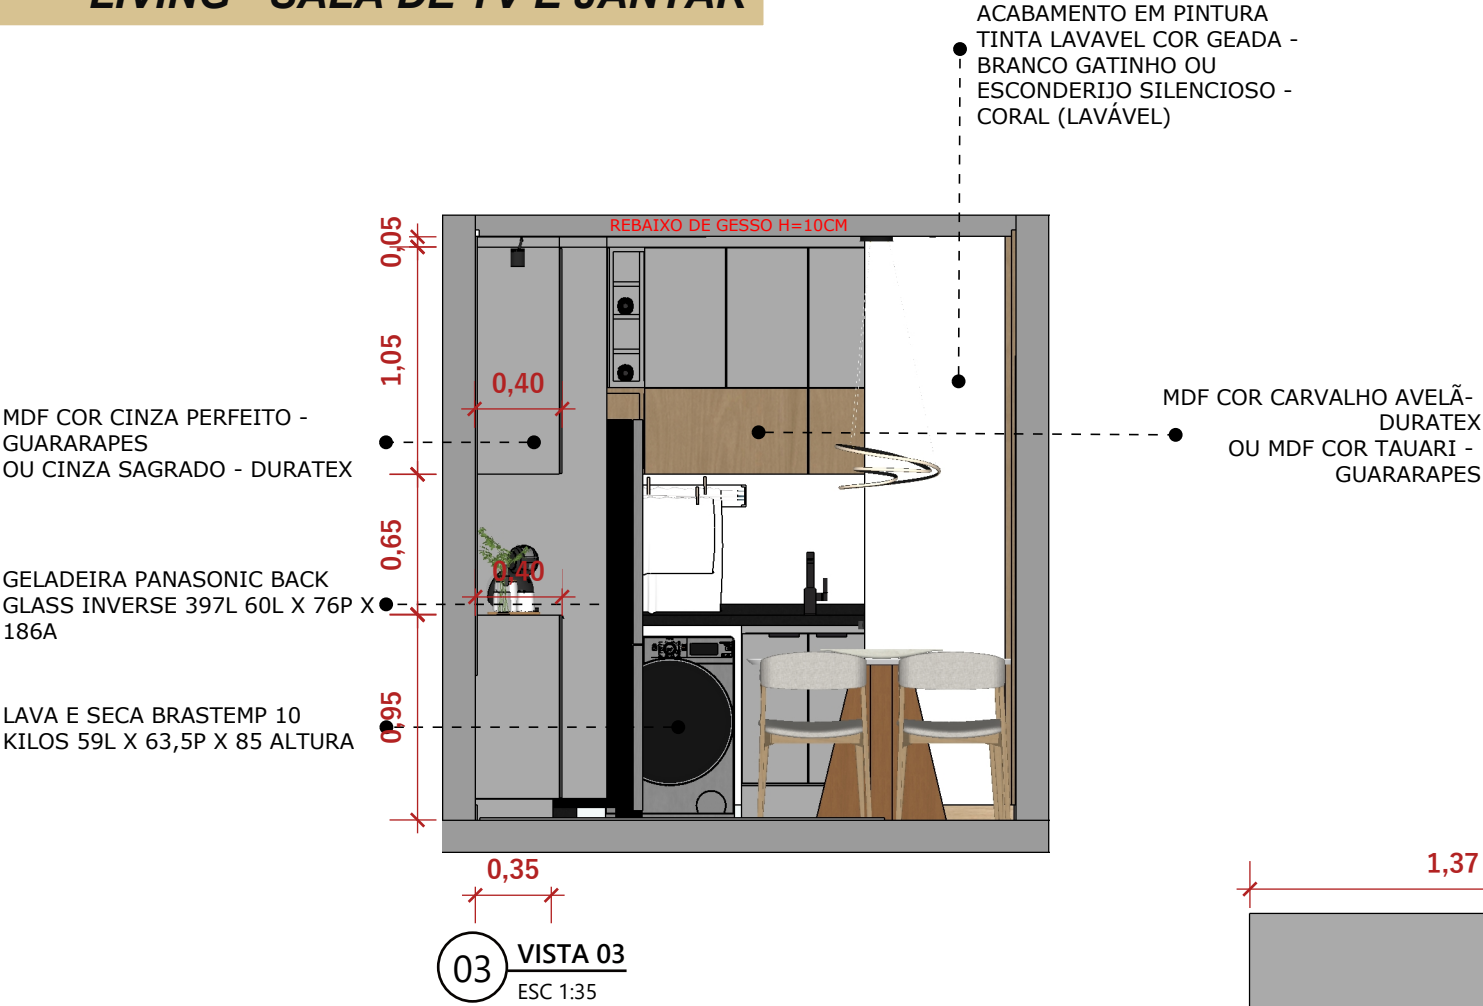

PERSPECTIVA PAINEL - SALA DE TV
ESC 1:25

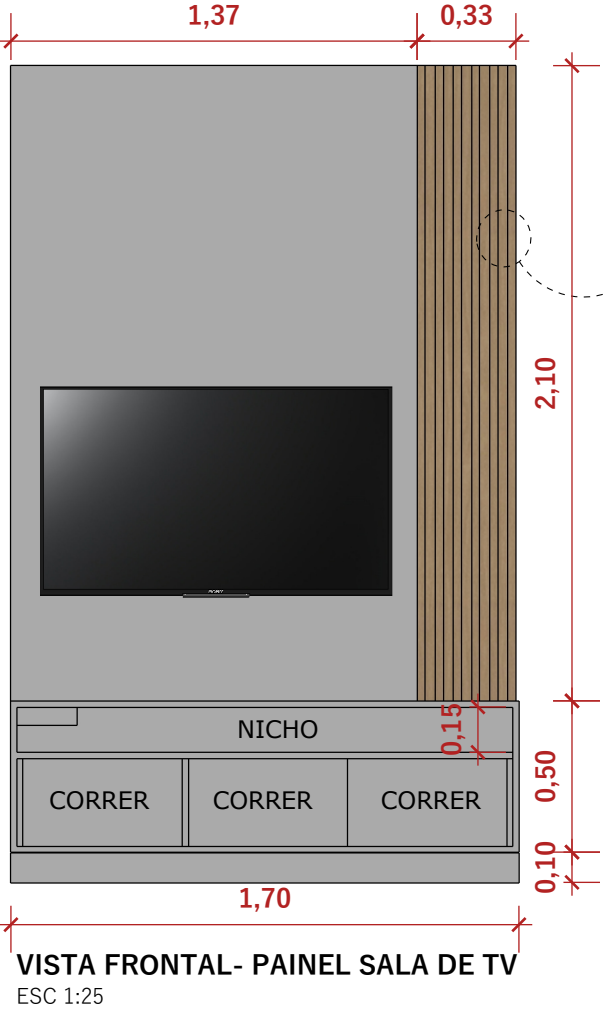

DET 01:
RIPADO 0,03CM DE
ESPESSURA E 0,03CM
DE ESPASSAMENTO

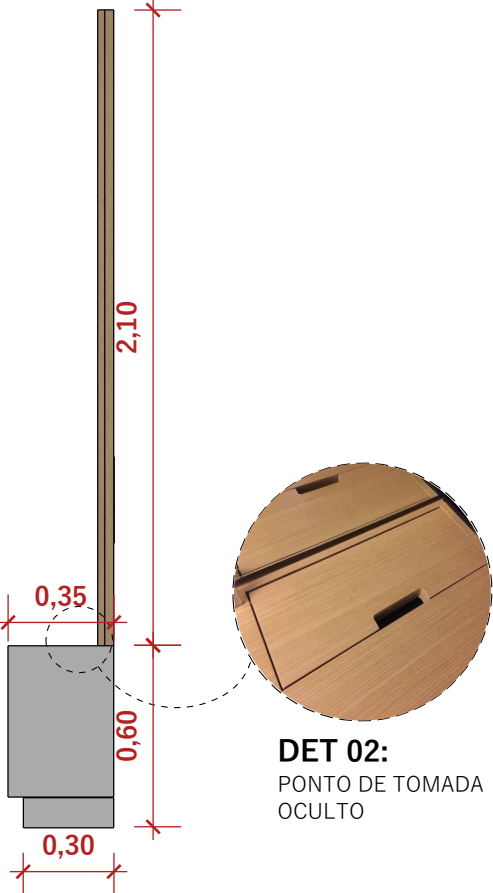

DET 02:
PONTO DE TOMADA
OCULTO



@STEFANIEFELIX.INTERIORES

****CONFERIR TODAS AS MEDIDAS NO LOCAL****
A DESIGNER NÃO SE RESPONSABILIZA POR
DIFERENÇAS DE MEDIDAS ENTRE PROJETO E OBRA;
VALOR DA COTA PREVALECE SOBRE A ESCALA;
DÚVIDAS FALAR COM A DESIGNER.

SF.STEFANIEFELIX@GMAIL.COM

PROJETO DE INTERIORES

LIVING - VISTAS COM COTAS

CLIENTE
GUSTAVO PATATIVA

DESIGNER
STEFANIE FELIX

LOCAL
MRV - LUZ DO CAMPO

DATA
26/04/2024

(19) 99577-3340


COZINHA E LAVANDERIA



05 VISTA 05
ESC 1:50




06 VISTA 06
ESC 1:50

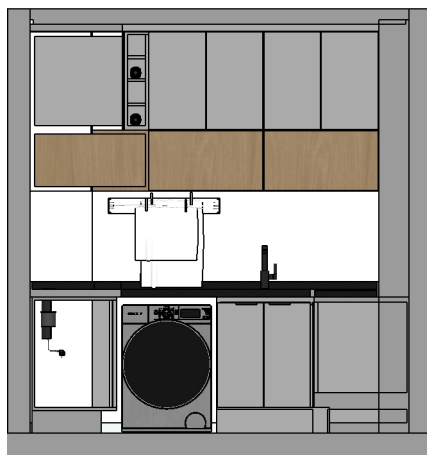


07 VISTA 07
ESC 1:50


- ESPAÇO PARA VINHOS
MDF COR CINZA PERFEITO -
GUARARAPES
OU CINZA SAGRADO - DURATEX
- MDF COR CARVALHO AVELÃ-
DURATEX
OU MDF COR TAUARI -
GUARARAPES
- VARAL INVISIVEL 0,70CM
- GRANITO COR SÃO GABRIEL
PRETO POLIDO
- MDF COR CINZA PERFEITO -
GUARARAPES
OU CINZA SAGRADO - DURATEX
- GAVETÃO IGUAL AO DET.01 COM
RODINHAS

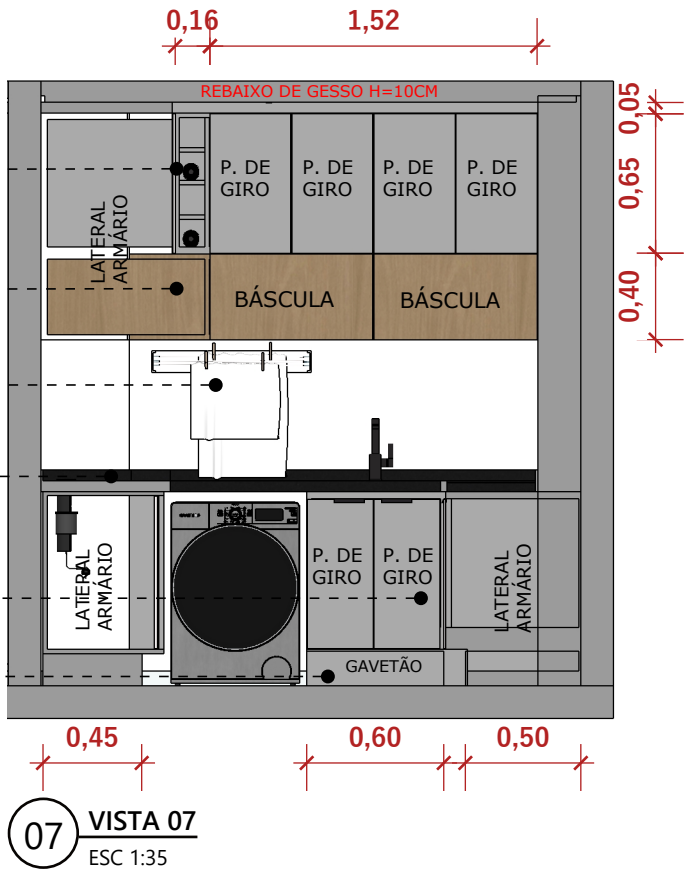

07 VISTA 07
ESC 1:35

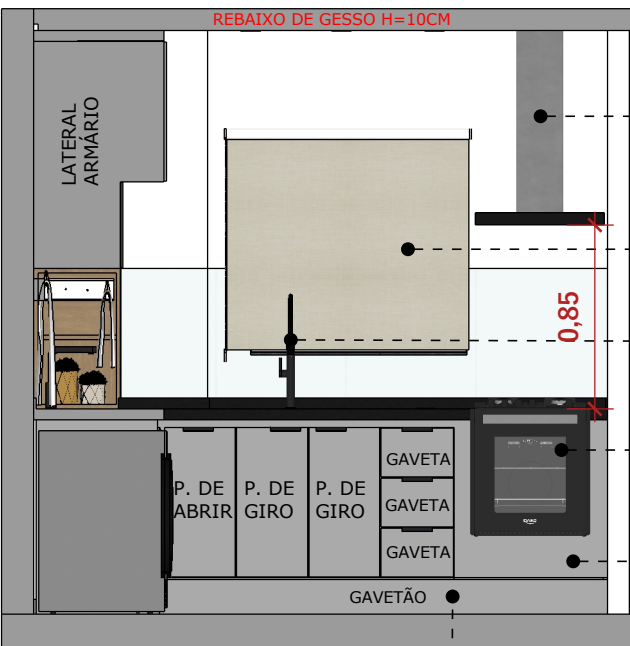


05 VISTA 05
ESC 1:35

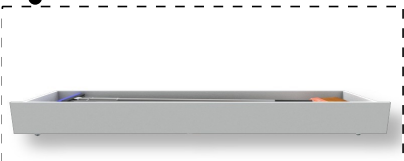

DET. 01 - GAVETA PARA
VASSOURAS COM RODINHAS
(RECUADO 15CM PARA O PÉ /
SAPATA)

- COIFA DE PAREDE 60CM INOX -
ELECTROLUX
- PERSIANA ROLO 100% BLACKOUT
LINHO BEGE
CONFIRMAR TAMANHO DA JANELA
- MISTURADOR MONOCOMANDO
GOURMET PRETO
- FOGÃO DE EMBUTIR 4 BOCAS
PRETO COM MESA DE VIDRO
55,5X65X64 ALTURA
- MDF COR CINZA PERFEITO -
GUARARAPES
OU CINZA SAGRADO - DURATEX

- PORTA COM VIDRO REFLECTA
FUME E ACABAMENTO NAS
LATERAIS DE MARCENARIA
- PREVER PERFIL DE LED E PONTOS
DE TOMADA EM CIMA DO BALCÃO
- MDF COR CARVALHO AVELÃ-
DURATEX
OU MDF COR TAUARI -
GUARARAPES
- GELADEIRA PANASONIC BACK
GLASS INVERSE 397L 60L X 76P X
186A
- MDF COR CINZA PERFEITO -
GUARARAPES
OU CINZA SAGRADO - DURATEX

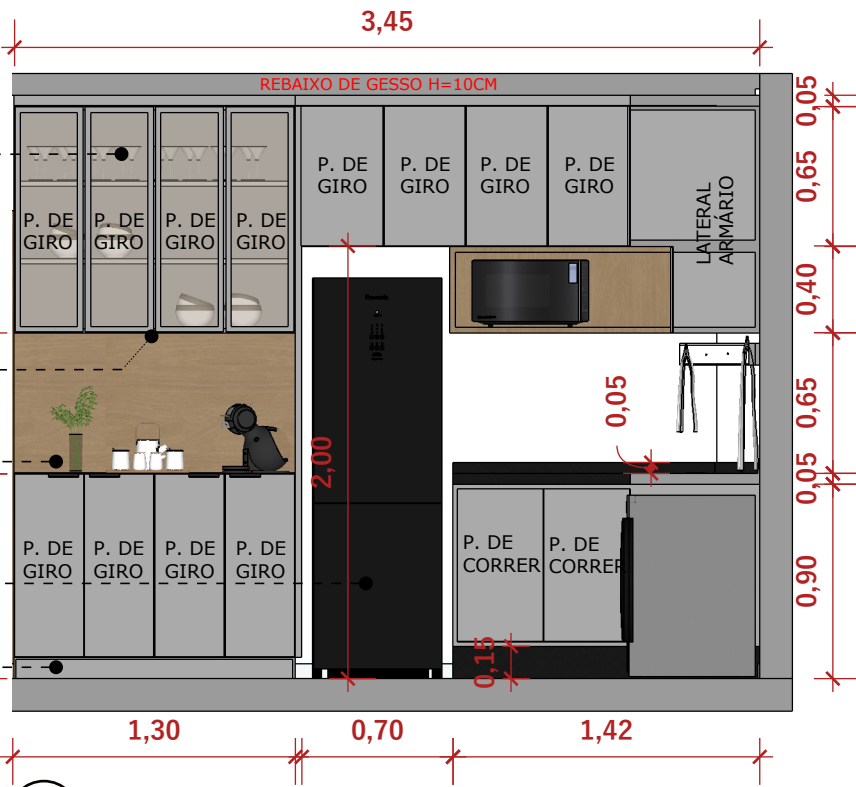

06 VISTA 06
ESC 1:35



@STEFANIEFELIX.INTERIORES

SF.STEFANIEFELIX@GMAIL.COM

****CONFERIR TODAS AS MEDIDAS NO LOCAL****
A DESIGNER NÃO SE RESPONSABILIZA POR
DIFERENÇAS DE MEDIDAS ENTRE PROJETO E OBRA;
VALOR DA COTA PREVALECE SOBRE A ESCALA;
DÚVIDAS FALAR COM A DESIGNER.

PROJETO DE INTERIORES
COZINHA/LAVANDERIA - VISTAS E DETALHAMENTO


CLIENTE
GUSTAVO PATATIVA
DESIGNER
STEFANIE FELIX

LOCAL
MRV - LUZ DO CAMPO
DATA
26/04/2024

(19) 99577-3340

FOLHA
08/15

COZINHA E LAVANDERIA

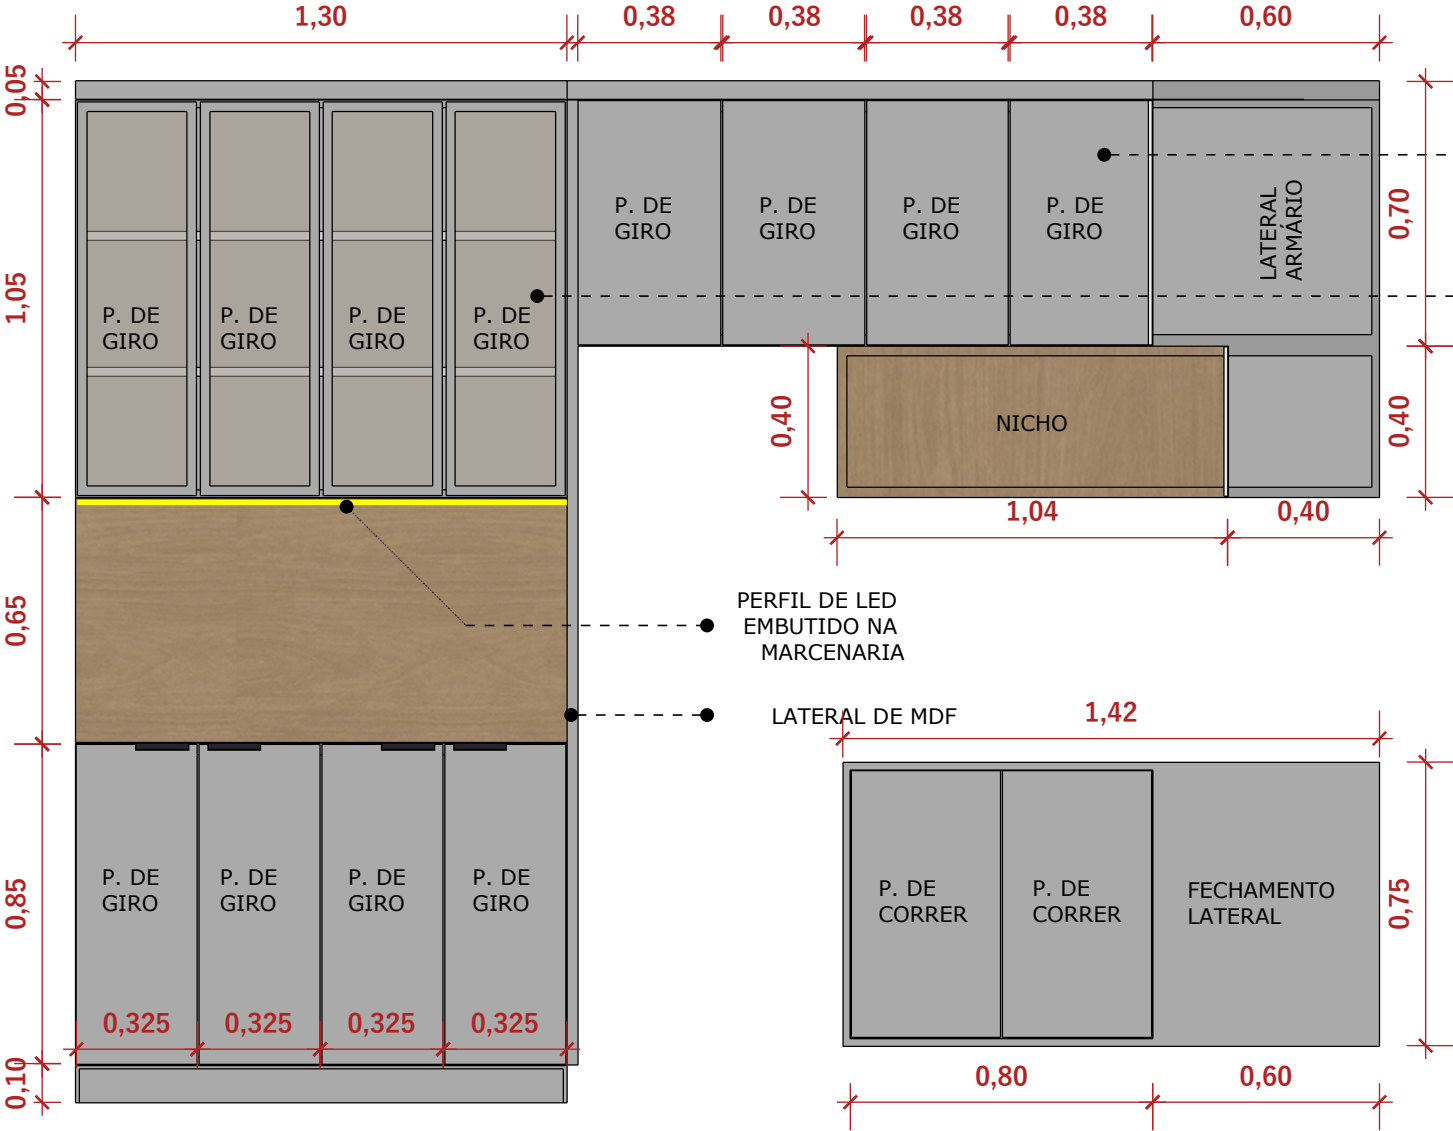


VISTA A
ESC 1:20

OBS: PREVER PONTOS DE ELÉTRICA CONFORME DETALHAMENTO DE MARMORARIA
TODAS AS PORTAS SEM TAMPONAMENTO




DET. 01 - GAVETA INTERNA DUPLA

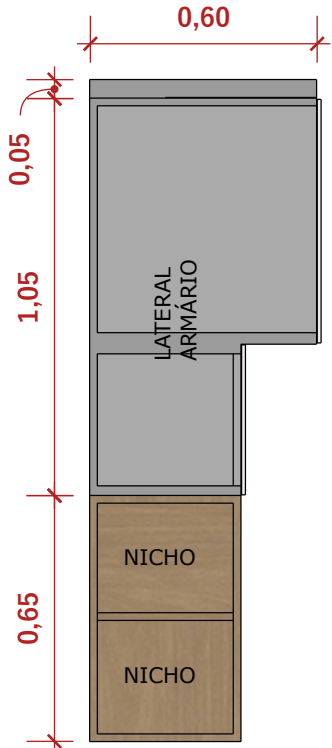


VISTA B
ESC 1:20



DET. 03 - PORTA PARA LIXO E GAVETA PEQUENA OCULPA

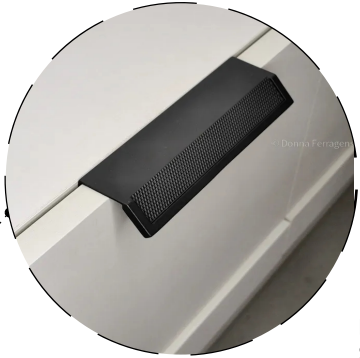

DET. 02:
PUXADOR ALÇA DE SOBREPOR 45° PRETO

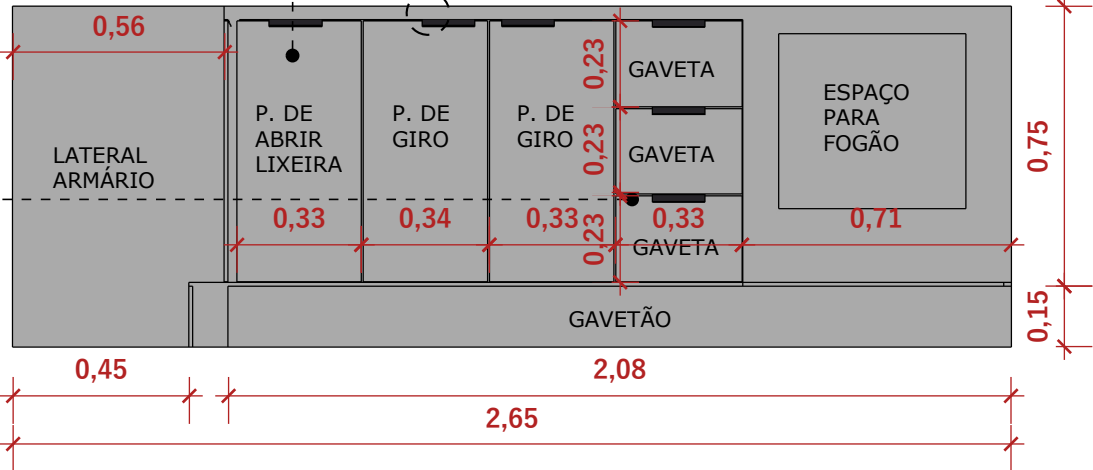

@STEFANIEFELIX.INTERIORES

****CONFERIR TODAS AS MEDIDAS NO LOCAL****
A DESIGNER NÃO SE RESPONSABILIZA POR DIFERENÇAS DE MEDIDAS ENTRE PROJETO E OBRA;
VALOR DA COTA PREVALECE SOBRE A ESCALA;
DÚVIDAS FALAR COM A DESIGNER.

SF.STEFANIEFELIX@GMAIL.COM

PROJETO DE INTERIORES
COZINHA/LAVANDERIA - DETALHAMENTO


CLIENTE
GUSTAVO PATATIVA
DESIGNER
STEFANIE FELIX

(19) 99577-3340


LOCAL
MRV - LUZ DO CAMPO
DATA
26/04/2024

FOLHA
09/15


MARMORARIA - DETALHAMENTO

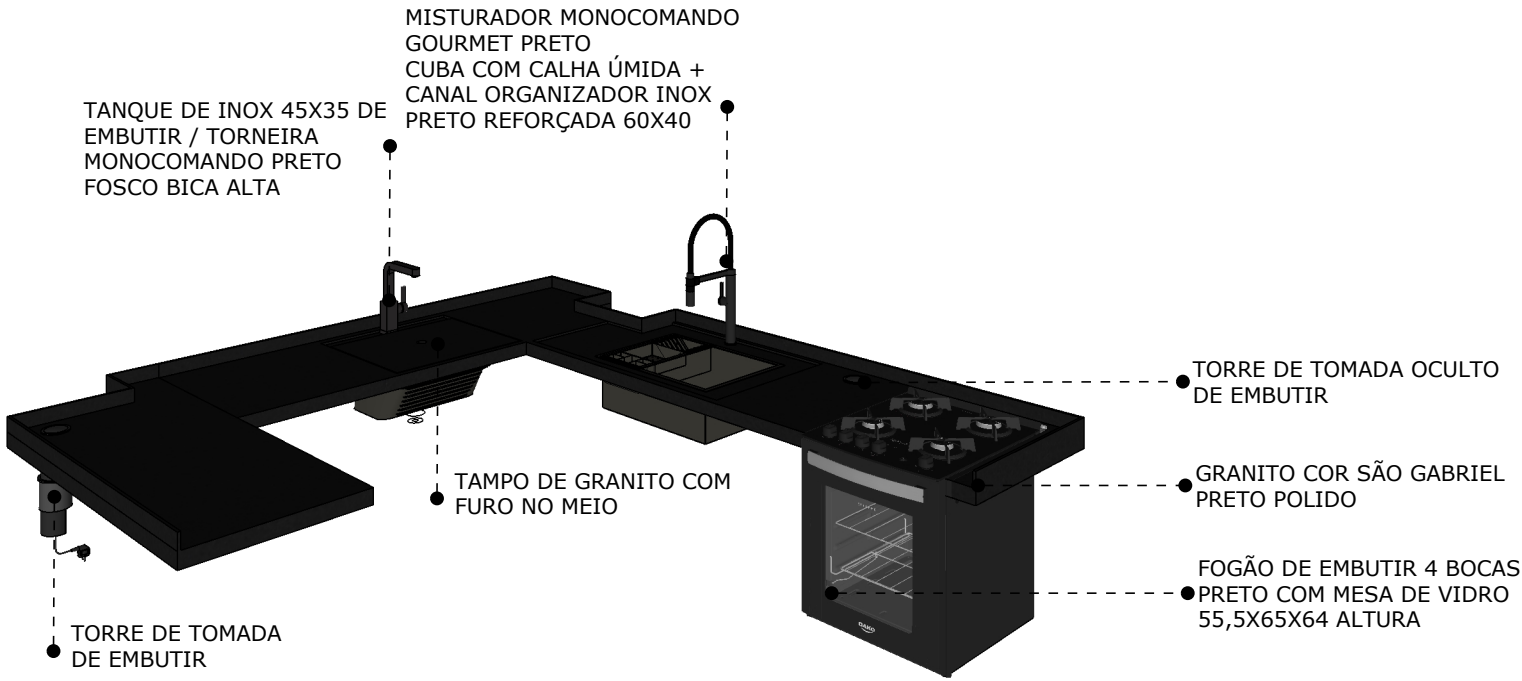


PERSPECTIVA - PIA E TANQUE
SEM ESCALA

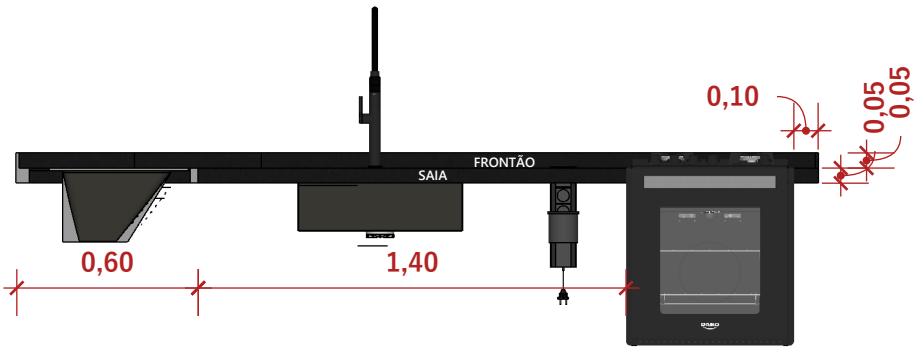

VISTA FRONTAL 01
ESC 1:25

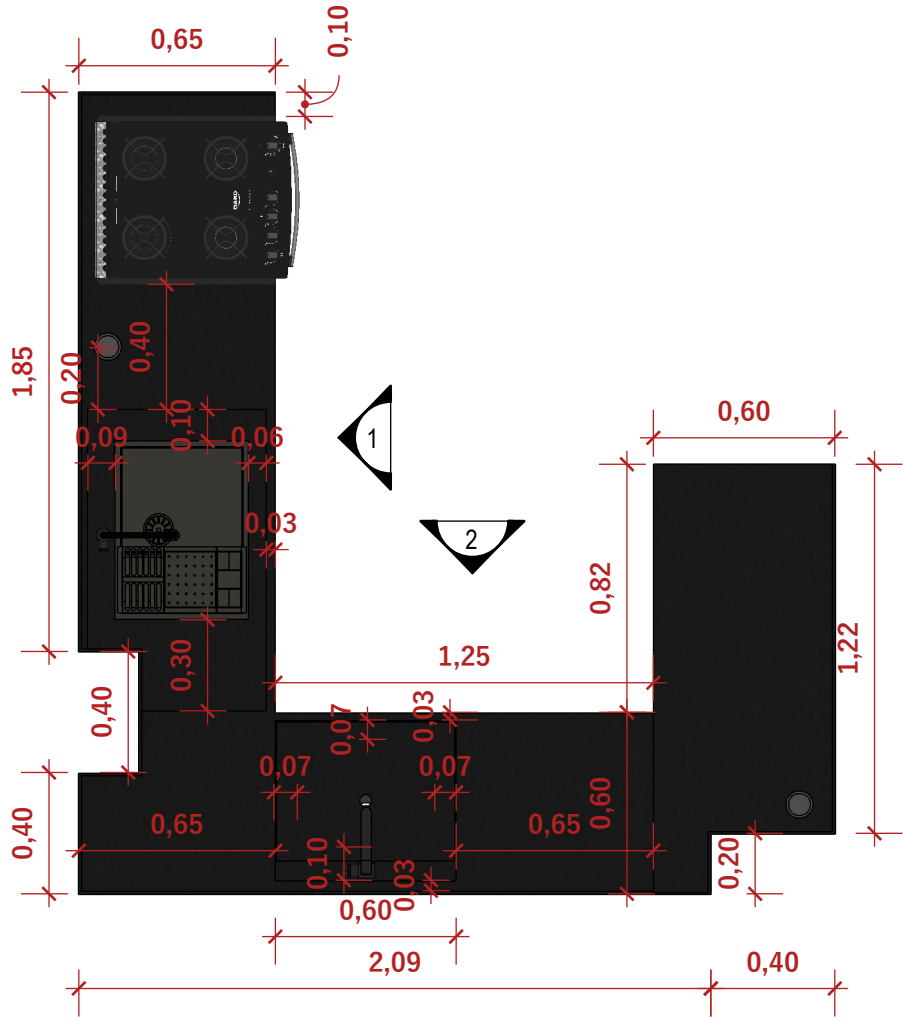

PLANTA BAIXA - BANCADA
ESC 1:25

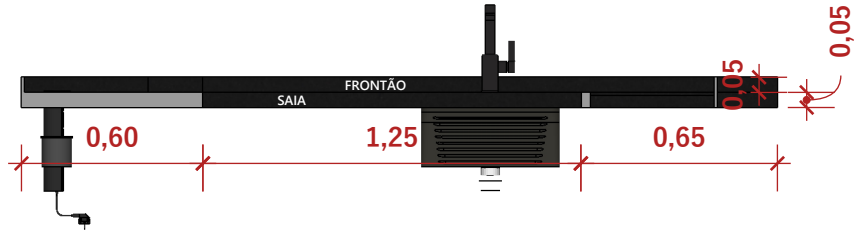

VISTA FRONTAL 02
ESC 1:25



@STEFANIEFELIX.INTERIORES

****CONFERIR TODAS AS MEDIDAS NO LOCAL****
A DESIGNER NÃO SE RESPONSABILIZA POR DIFERENÇAS DE MEDIDAS ENTRE PROJETO E OBRA; VALOR DA COTA PREVALECE SOBRE A ESCALA; DÚVIDAS FALAR COM A DESIGNER.

SF.STEFANIEFELIX@GMAIL.COM

PROJETO DE INTERIORES
MARMORARIA - DETALHAMENTO


CLIENTE
GUSTAVO PATATIVA
DESIGNER
STEFANIE FELIX

(19) 99577-3340


LOCAL
MRV - LUZ DO CAMPO
DATA
26/04/2024

FOLHA
10/15

QUARTO CASAL

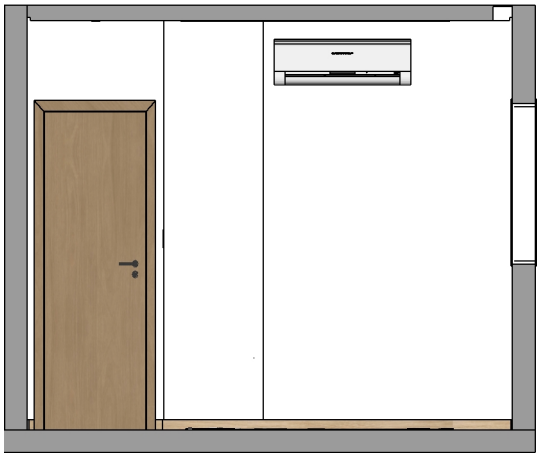


08 VISTA 08
ESC 1:50

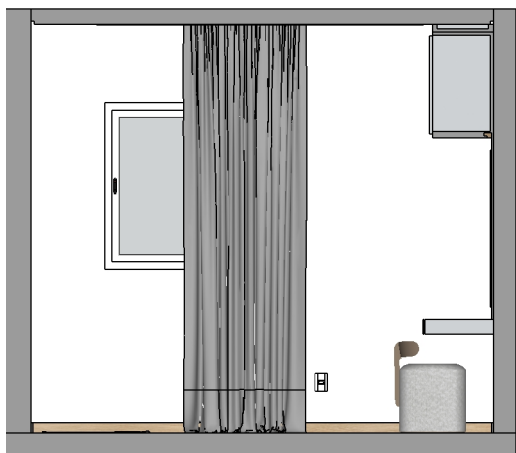


09 VISTA 09
ESC 1:50



10 VISTA 10
ESC 1:50

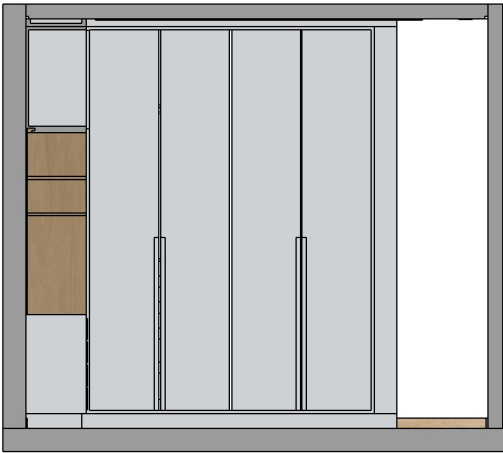


11 VISTA 11
ESC 1:50

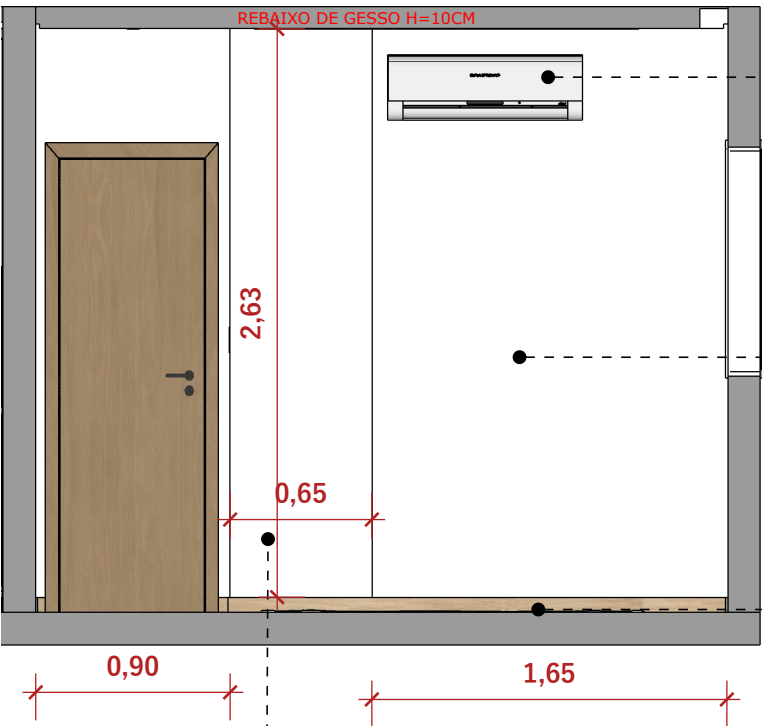

08 VISTA 08
ESC 1:35

- REBAIXO DE GESSO H=10CM
- AR CONDICIONADO(PREVER SE PODERÁ SER INSTALADO NESSA PAREDE)
- ACABAMENTO EM PINTURA TINTA LAVAVEL COR GEADA - BRANCO GATINHO OU ESCONDERIJO SILENCIOSO - CORAL (LAVÁVEL)
- TAPETE PASSADEIRA 180X65 COR NEUTRO ALGODÃO CRU ANTEDERRAPANTE
- ESPELHO SOB MEDIDA COR NATURAL

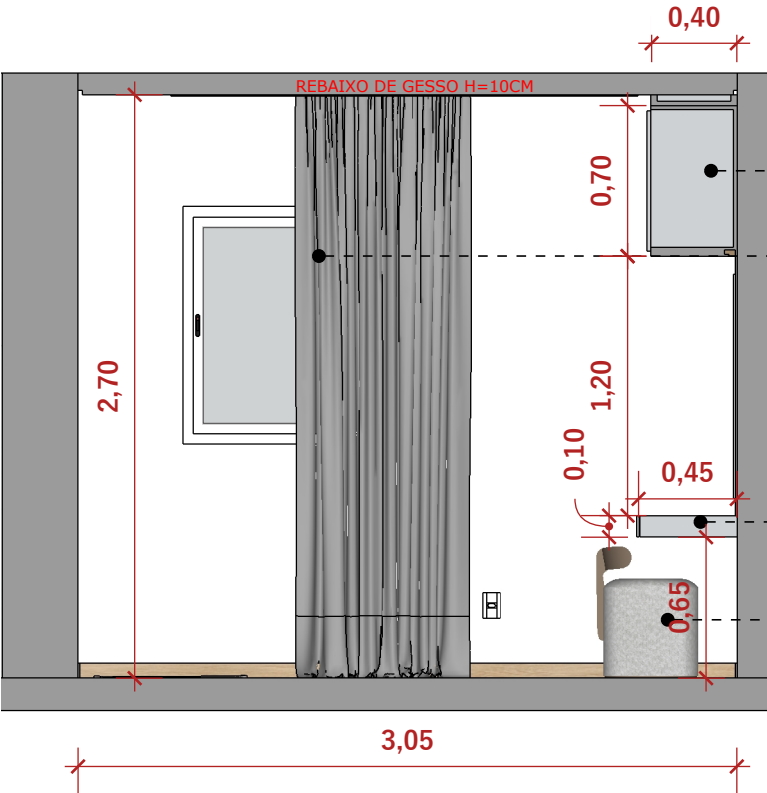

09 VISTA 09
ESC 1:35

- MDF COR CINZA NUVEM - GUARARAPES
- CORTINA COM TRILHO SUÍÇO BLACKOUT - COR CINZA MÉDIO
- LATERAL PENTEADEIRA DE MDF COR CINZA NUVEM - GUARARAPES
- PUFF INSPIRAÇÃO UMMA ESCAL



@STEFANIEFELIX.INTERIORES

****CONFERIR TODAS AS MEDIDAS NO LOCAL****
A DESIGNER NÃO SE RESPONSABILIZA POR DIFERENÇAS DE MEDIDAS ENTRE PROJETO E OBRA; VALOR DA COTA PREVALECE SOBRE A ESCALA; DÚVIDAS FALAR COM A DESIGNER.

SF.STEFANIEFELIX@GMAIL.COM

PROJETO DE INTERIORES
QUARTO CASAL - VISTAS HUMANIZADAS E COM COTAS


CLIENTE
GUSTAVO PATATIVA
DESIGNER
STEFANIE FELIX

LOCAL
MRV - LUZ DO CAMPO
DATA
26/04/2024

(19) 99577-3340


QUARTO CASAL

CAMA DE CASAL QUEEN SIZE
1,58X1,98

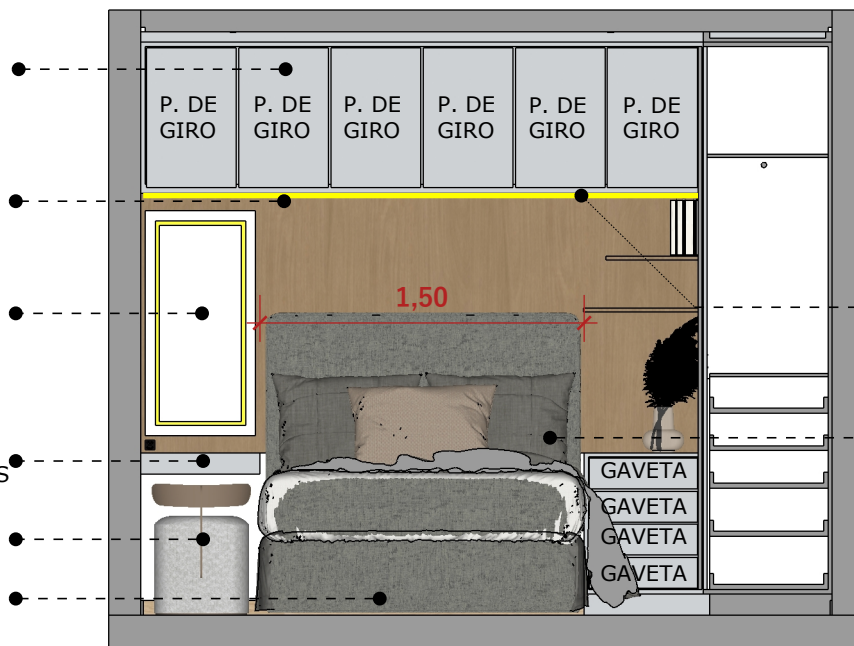


10 **VISTA 10**
ESC 1:35

CABECEIRA
ESTOFADA
DE LINHO
CINZA MÉDIO

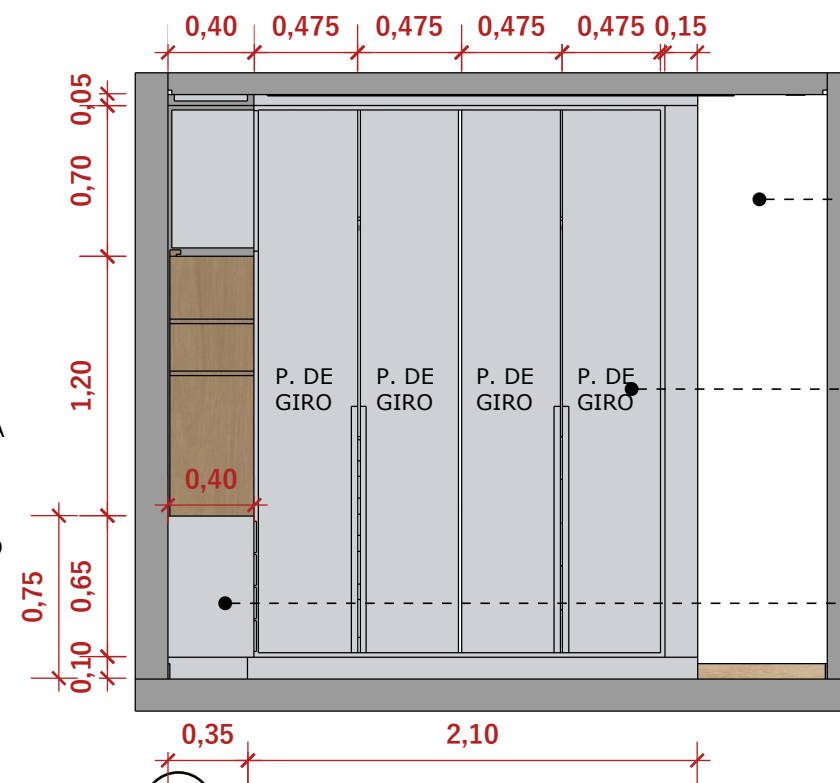

11 VISTA 11
ESC 1:35


LATERAL MESA LATERAL COM
GAVETAS DE MDF COR CINZA
● NUVEM - GUARARAPES / PREVER
RECUO NA PRIMEIRA GAVETA
PARA PONTOS DE TOMADAS
OCULTOS

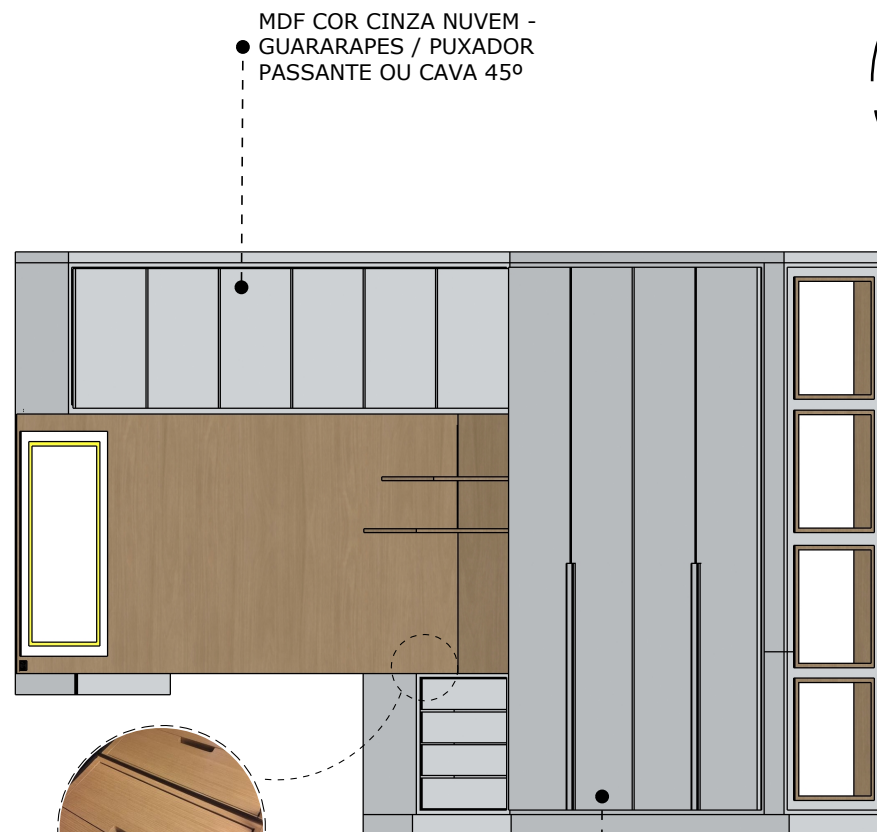

Technical drawing of a dressing room (Penteadeira) layout. The layout includes a central wooden panel (PAINEL DE MDF) with a width of 1,60m and a height of 1,20m. To the left of the panel is a row of six circular mirrors (P. DE GIRO) with a total width of 2,60m and a height of 0,70m. Below the mirrors is a row of four drawers (GAVETA) with a total width of 0,50m and a height of 0,10m. To the right of the panel is a row of four mirrors (ESPELHO) with a total width of 0,60m and a height of 0,70m. The overall dimensions of the dressing room are 2,60m wide and 2,70m high. The drawing also shows a door (PENTEADEIRA) with a width of 0,50m and a height of 0,10m, and a small table (DIVISÓRIA) with a width of 0,50m and a height of 0,10m.

VISTA FRONTAL GUARDA-ROUPA
ESCALA 1:35

PRATELEIRAS
DESLIZANTES EM ●
MELAMINA BRANCA

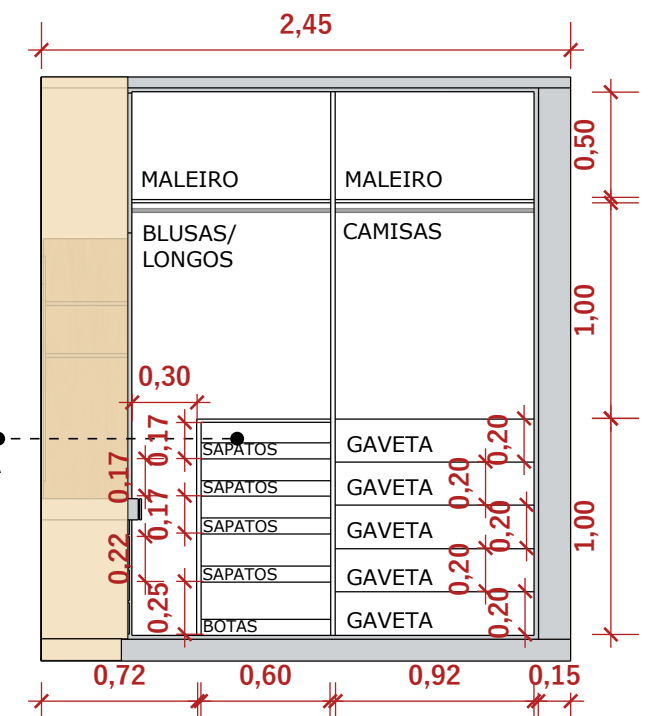

VISTA FRONTAL GUARDA-ROUPA ABERTO
ESCALA 1:35

DET 02:
PONTO DE TOMADA
OCULTO

**PERSPECTIVA - GUARDA-
ROUPA QUARTO CASAL**
ESCALA 1:35

PORTAS DE ABRIR COM
PUXADOR CAVA
● RETANGULARES NA
PRÓPRIA MARCENARIA



****CONFERIR TODAS AS MEDIDAS NO LOCAL****
A DESIGNER NÃO SE RESPONSABILIZA POR
DIFERENÇAS DE MEDIDAS ENTRE PROJETO E OBRA;
VALOR DA COTA PREVALECE SOBRE A ESCALA;
DÚVIDAS FALAR COM A DESIGNER.

PROJETO DE INTERIORES

QUARTO CASAL - VISTAS E DETALHAMENTO

CLIENTE
GUSTAVO PATATIVA

DESIGNER
STEFANIE FELIX

LOCAL
MRV - LUZ DO CAMPO

DATA
26/04/2024


FOLHA
12/15

@STEFANIEFELIX.INTERIORES


SF.STEFANIEFELIX@GMAIL.COM

(19) 99577-3340

QUARTO HOME OFFICE

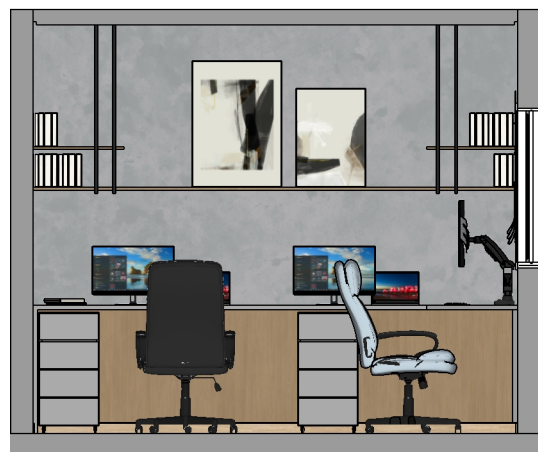


12 VISTA 12
ESC 1:50

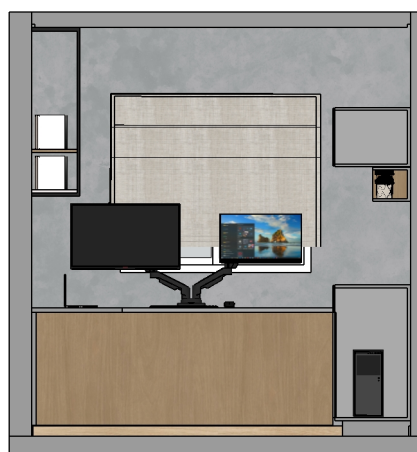


13 VISTA 13
ESC 1:50




14 VISTA 14
ESC 1:50

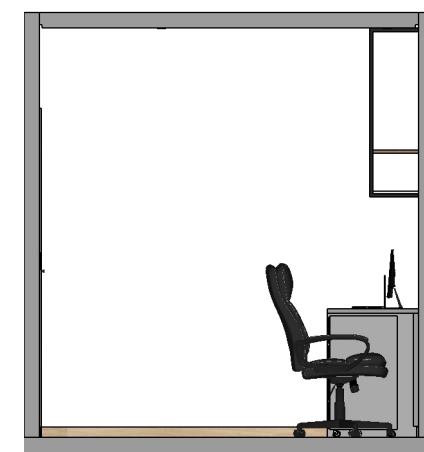

15 VISTA 15
ESC 1:50

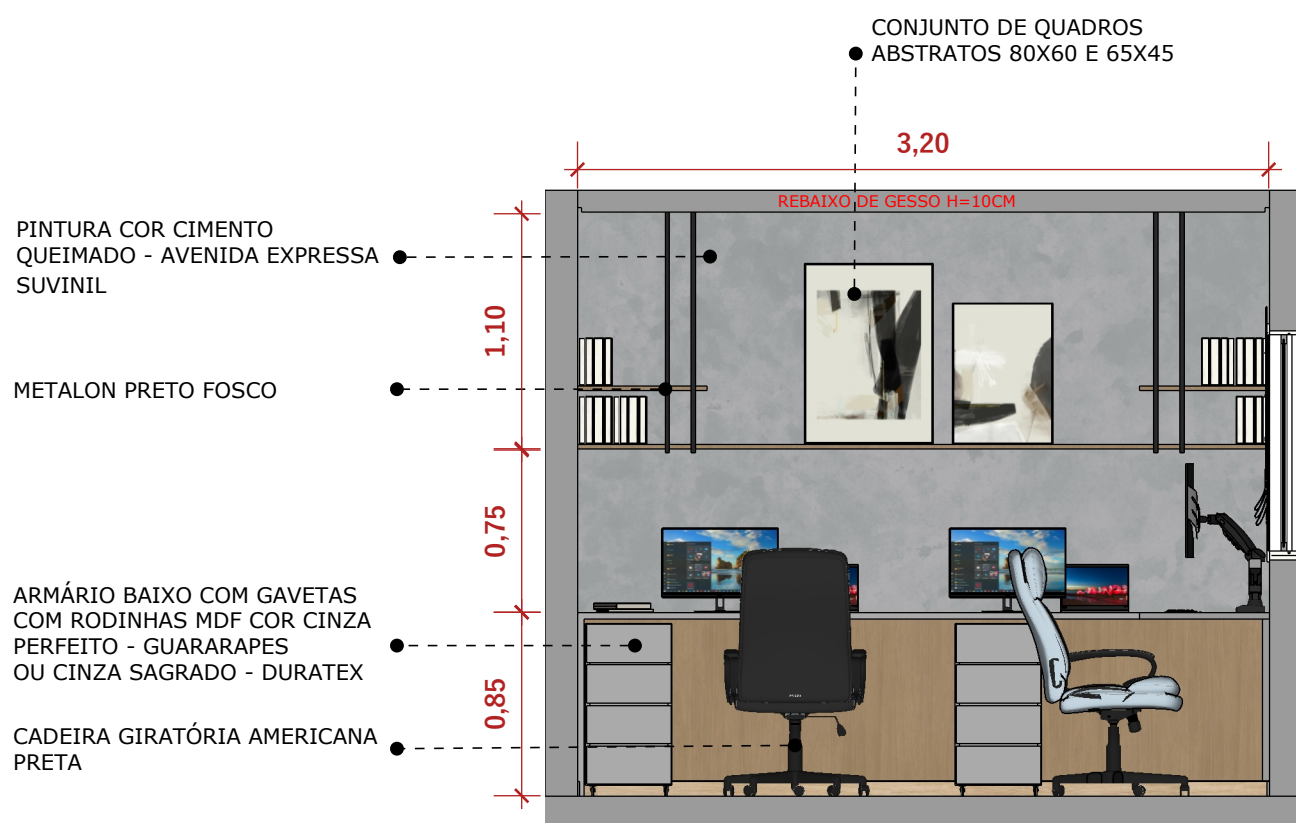

12 VISTA 12
ESC 1:35

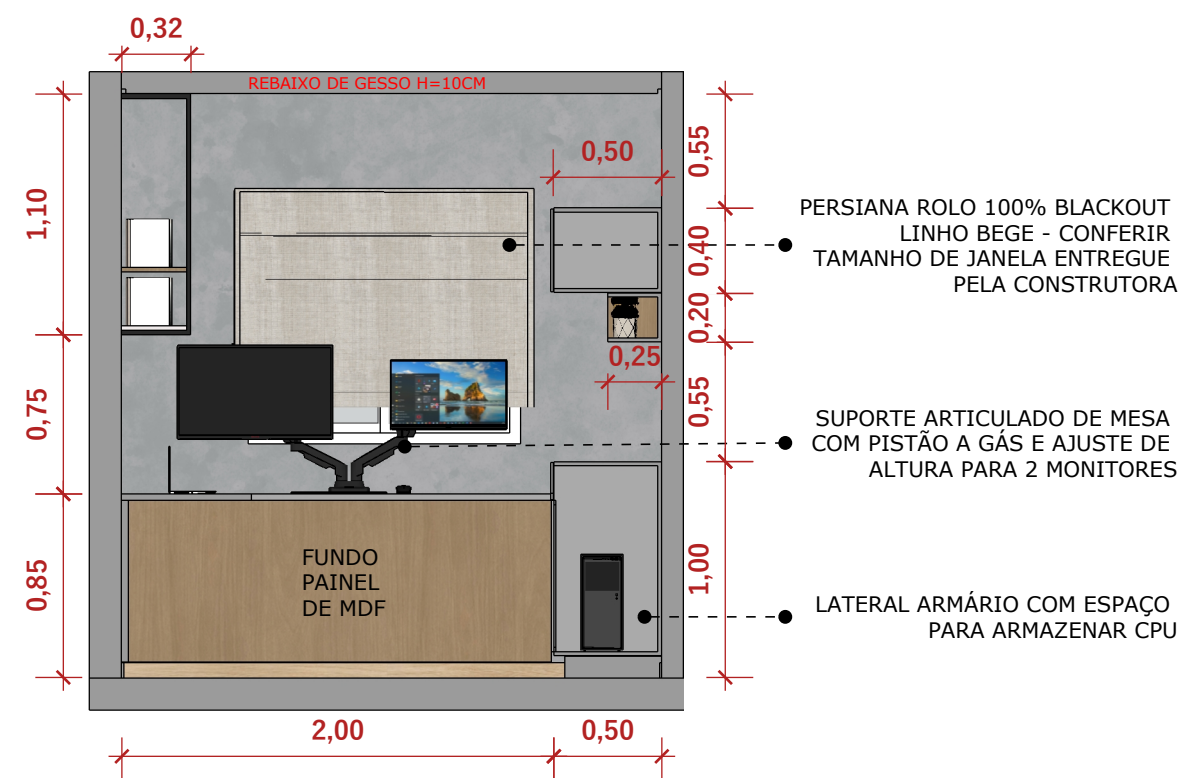

13 VISTA 13
ESC 1:35



@STEFANIEFELIX.INTERIORES

****CONFERIR TODAS AS MEDIDAS NO LOCAL****
A DESIGNER NÃO SE RESPONSABILIZA POR
DIFERENÇAS DE MEDIDAS ENTRE PROJETO E OBRA;
VALOR DA COTA PREVALECE SOBRE A ESCALA;
DÚVIDAS FALAR COM A DESIGNER.

SF.STEFANIEFELIX@GMAIL.COM

PROJETO DE INTERIORES

HOME OFFICE - VISTAS HUMANIZADAS E COM COTAS

CLIENTE
GUSTAVO PATATIVA

DESIGNER
STEFANIE FELIX

(19) 99577-3340

LOCAL
MRV - LUZ DO CAMPO

DATA
26/04/2024

FOLHA
13/15

QUARTO HOME OFFICE


ACABAMENTO EM PINTURA TINTA LAVAVEL COR GEADA - BRANCO GATINHO OU ESCONDERIJO SILENCIOSO - CORAL (LAVÁVEL)

MDF COR CINZA PERFEITO - GUARARAPES OU CINZA SAGRADO - DURATEX


BEBEDOURO DE ÁGUA GELADA OU FRIA COM GALÃO DE ÁGUA (PREVER PONTO DE ELÉTRICA PARA FAZER A LIGAÇÃO E CONFERIR MODELO ESCOLHIDO PARA DEFINIÇÃO DA ALTURA VÃO DA PORTA)

VASO COM VEGETAÇÃO

RIPADO VASADO PARA CIRCULAÇÃO DE AR DO CPU

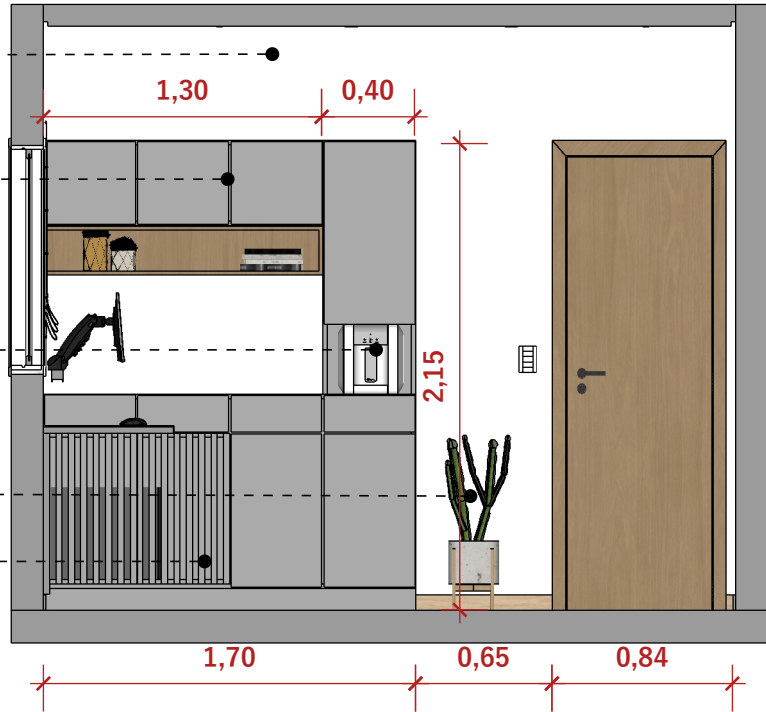

14 VISTA 14
ESC 1:35

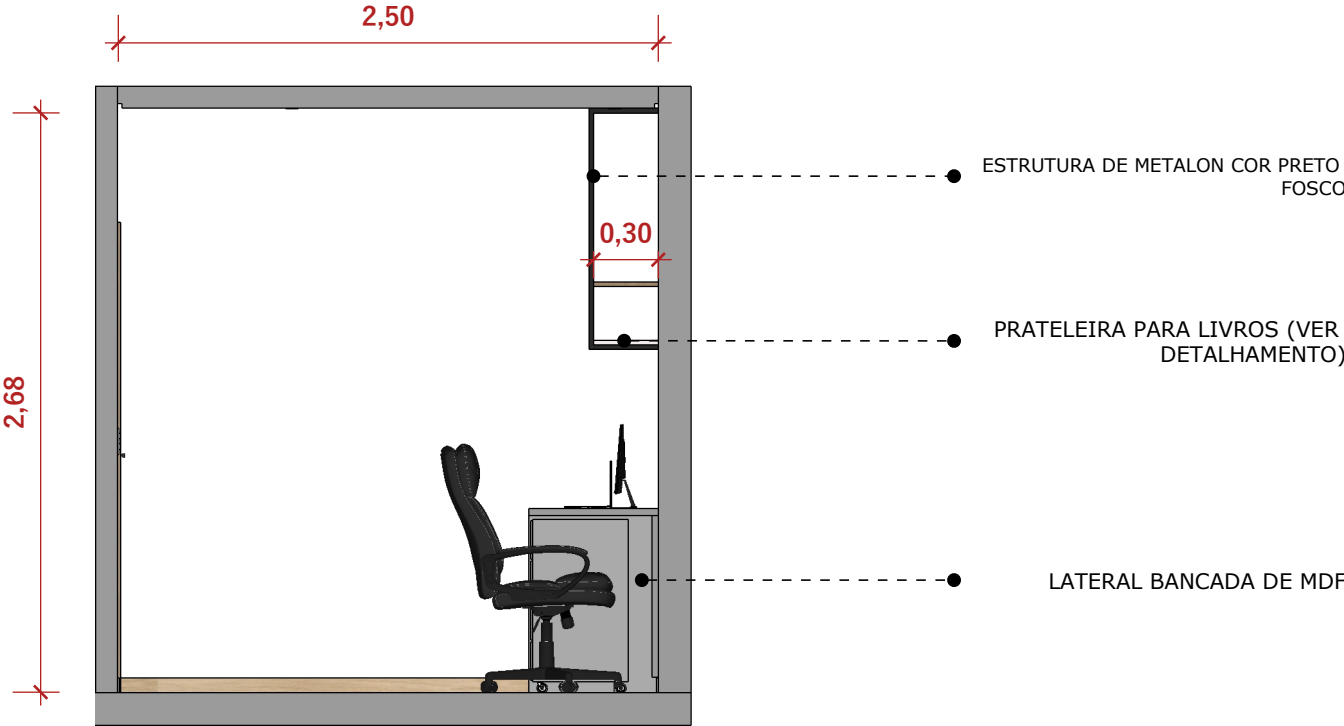


15 VISTA 15
ESC 1:35

ESTRUTURA DE METALON COR PRETO FOSCO

PRATELEIRA PARA LIVROS (VER DETALHAMENTO)

LATERAL BANCADA DE MDF

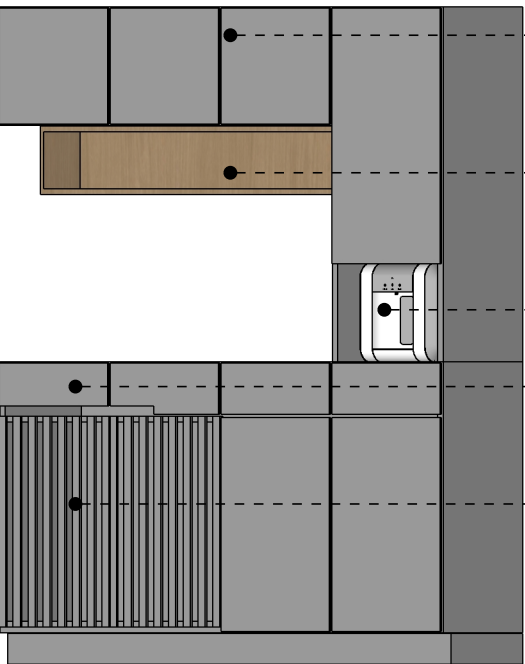

PERSPECTIVA - ARMÁRIO HOME OFFICE
ESC 1:25


MDF COR CINZA PERFEITO - GUARARAPES OU CINZA SAGRADO - DURATEX COM PUXADOR PASSANTE OU CAVA 45º

MDF COR CARVALHO AVELÃ - DURATEX OU MDF COR TAUARI - GUARARAPES


ESPAÇO PARA BEBEDOURO DE ÁGUA

GAVETAS FALSAS SOBREPOSTAS A MESA DE MDF


PORTA COM FRENTE RIPADO VASADO PARA CIRCULAÇÃO DE AR DO CPU

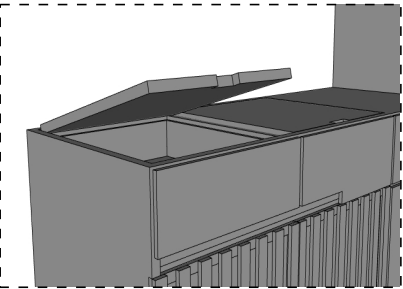


DET. 01 - TAMPO DE ABRIR PARA CIMA OCULTA PARA REAPROVEITAMENTO DE ESPAÇO COM PISTÃO A GÁS

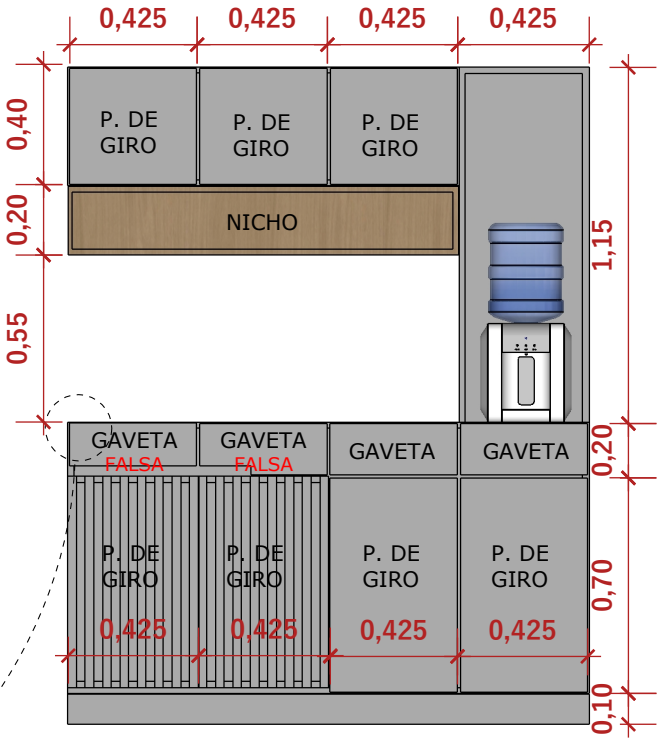

VISTA FRONTAL - ARMÁRIO HOME OFFICE
ESC 1:25

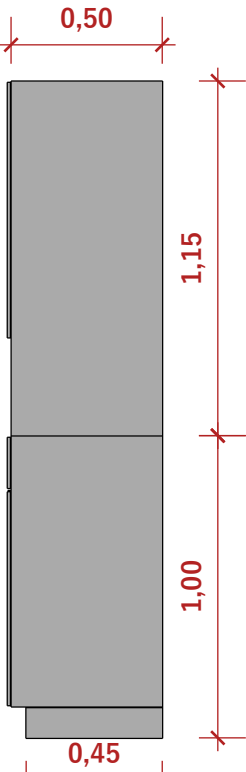

VISTA LATERAL - ARMÁRIO
ESC 1:25

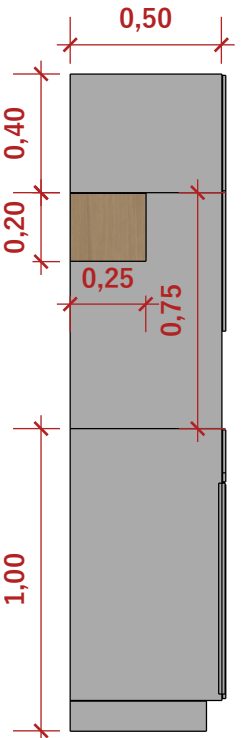

VISTA LATERAL - ARMÁRIO
ESC 1:25



@STEFANIEFELIX.INTERIORES

****CONFERIR TODAS AS MEDIDAS NO LOCAL****
A DESIGNER NÃO SE RESPONSABILIZA POR DIFERENÇAS DE MEDIDAS ENTRE PROJETO E OBRA; VALOR DA COTA PREVALECE SOBRE A ESCALA; DÚVIDAS FALAR COM A DESIGNER.

SF.STEFANIEFELIX@GMAIL.COM

PROJETO DE INTERIORES

HOME OFFICE - VISTAS HUMANIZADAS E DETALHAMENTO

CLIENTE
GUSTAVO PATATIVA

DESIGNER
STEFANIE FELIX

LOCAL
MRV - LUZ DO CAMPO


DATA
26/04/2024

(19) 99577-3340


QUARTO HOME OFFICE




PERSPECTIVA - MESA HOME OFFICE
ESCALA 1:25

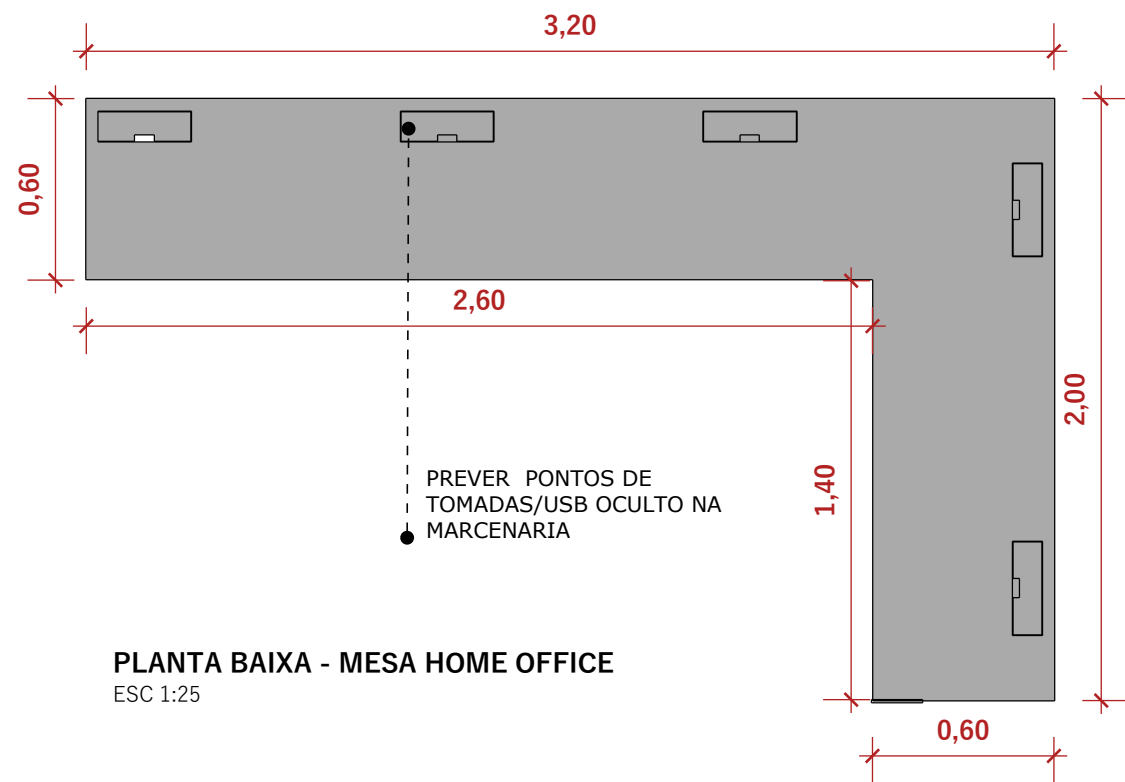


PLANTA BAIXA - MESA HOME OFFICE
ESC 1:25

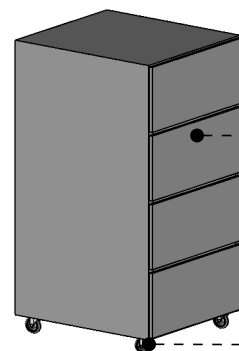


PERSPECTIVA - GAVETAS
ESC 1:20

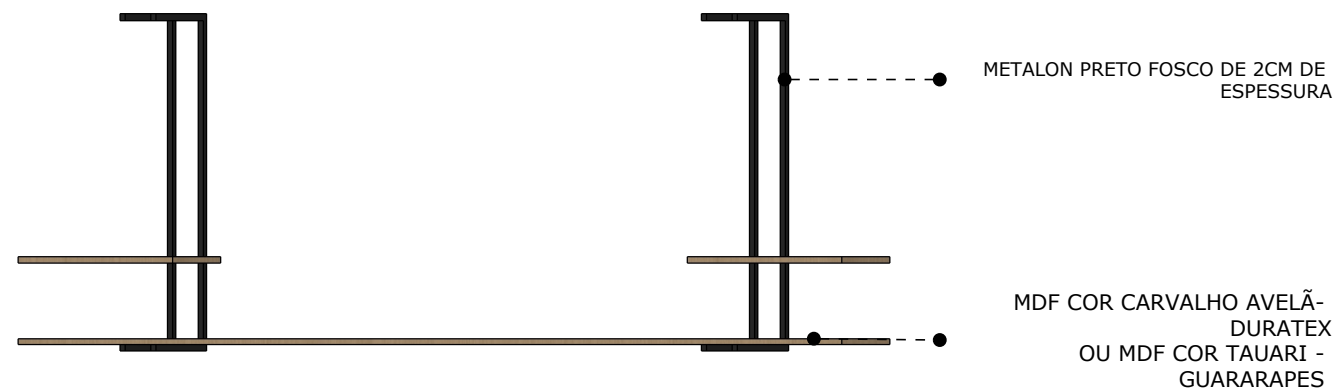


PERSPECTIVA - PRATELEIRA HOME OFFIC
EESCALA 1:25

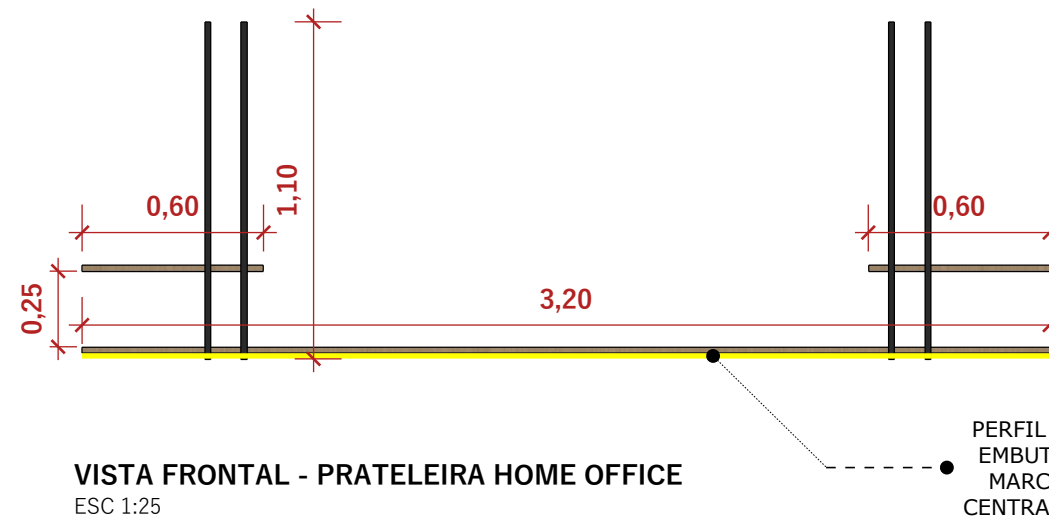


VISTA FRONTAL - PRATELEIRA HOME OFFICE
ESC 1:25

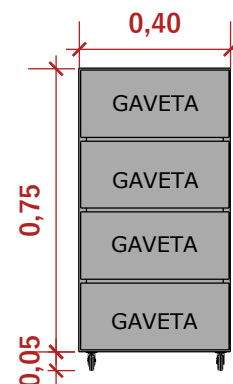

VISTA FRONTAL - GAVETAS
ESC 1:20

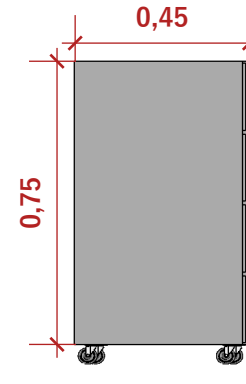

VISTA LATERAL - GAVETAS
ESC 1:20

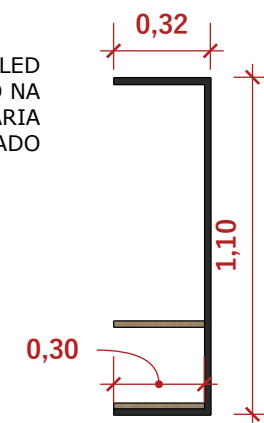

VISTA LATERAL - PRATELEIRA HOME OFFICE
ESC 1:25



@STEFANIEFELIX.INTERIORES

****CONFERIR TODAS AS MEDIDAS NO LOCAL****
A DESIGNER NÃO SE RESPONSABILIZA POR DIFERENÇAS DE MEDIDAS ENTRE PROJETO E OBRA; VALOR DA COTA PREVALECE SOBRE A ESCALA; DÚVIDAS FALAR COM A DESIGNER.

SF.STEFANIEFELIX@GMAIL.COM

PROJETO DE INTERIORES
HOME OFFICE - DETALHAMENTO

CLIENTE
GUSTAVO PATATIVA
DESIGNER
STEFANIE FELIX

(19) 99577-3340

LOCAL
MRV - LUZ DO CAMPO
DATA
26/04/2024

FOLHA
15/15